
## DAFTAR ISI


| NO | JUDUL GAMBAR | KETERANGAN | NO. HAL |
|---|---|---|---|
| 01 | SITE PLAN | | 01 |
| 02 | SITE SITUASI | | 02 |
| 03 | RENCANA PENGAMBILAN SIKU BANGUNAN | | 03 |
| 04 | DENAH LANTAI 01 | | 04 |
| 05 | DENAH LANTAI 02 | | 05 |
| 06 | DENAH LANTAI 03 | | 06 |
| 07 | DENAH LANTAI 04 | | 07 |
| 08 | DENAH LANTAI ATAP | | 08 |
| 09 | TAMPAK ATAS | | 09 |
| 10 | TAMPAK A | | 10 |
| 11 | TAMPAK B | | 11 |
| 12 | TAMPAK C | | 12 |
| 13 | TAMPAK D | | 13 |
| 14 | POTONGAN A - A | | 14 |
| 15 | POTONGAN B - B | | 15 |
| 16 | POTONGAN C - C | | 16 |
| 17 | POTONGAN D - D | | 17 |
| 18 | POTONGAN E - E | | 18 |
| 19 | DETAIL DENAH LANTAI 01 | | 19 |
| 20 | DETAIL DENAH LANTAI 02 | | 20 |
| 21 | DETAIL DENAH LANTAI 03 | | 21 |
| 22 | DETAIL DENAH LANTAI 04 | | 22 |
| 23 | RENCANA FINISHING LANTAI, LT. 01 | | 23 |
| 24 | RENCANA FINISHING LANTAI, LT. 02 | | 24 |
| 25 | RENCANA FINISHING LANTAI, LT. 03 | | 25 |
| 26 | RENCANA FINISHING LANTAI, LT. 04 | | 26 |
| 27 | RENCANA FINISHING LANTAI, LT. ATAP | | 27 |
| 28 | RENCANA FINISHING LANTAI, LT. ATAP | | 28 |
| 29 | DETAIL - DETAIL FINISHING | | 29 |
| 30 | DETAIL JAMB LIFT | | 30 |
| 31 | RENCANA PLAFON LANTAI 01 (ELV. +3.000) | | 31 |
| 32 | RENCANA PLAFON LANTAI 01 (ELV. +3.200) | | 32 |
| 33 | RENCANA PLAFON LANTAI 02 (ELV. +7.200) | | 33 |
| 34 | RENCANA PLAFON LANTAI 02 (ELV. +7.400) | | 34 |
| 35 | RENCANA PLAFON LANTAI 03 (ELV. +11.400) | | 35 |
| 36 | RENCANA PLAFON LANTAI 03 (ELV. +11.600) | | 36 |
| 37 | RENCANA PLAFON LANTAI 04 (ELV. +15.600) | | 37 |
| 38 | RENCANA PLAFON LANTAI 04 (ELV. +15.800) | | 38 |
| 39 | RENCANA PERKUATAN PLAFON | | 39 |
| 40 | DETAIL PLAFON LOBBY | | 40 |
| 41 | RENCANA PLAFON CO-WORKING LT. 02 | | 41 |
| 42 | RENCANA PLAFON CO-WORKING LT. 02 | | 42 |
| 43 | RENCANA PLAFON CO-WORKING LT. 03 | | 43 |
| 44 | RENCANA PLAFON CO-WORKING LT. 03 | | 44 |
| 45 | RENCANA PLAFON PRE-FUNCTION LT. 04 | | 45 |
| 46 | RENCANA PLAFON PRE-FUNCTION LT. 04 | | 46 |
| 47 | DETAIL PLAFON R. CINEMA | | 47 |
| 48 | RENCANA PLAFON AREA WASTAFEL TOILET | | 48 |
| 49 | POTONGAN PLAFON AREA WASTAFEL TOILET | | 49 |
| 50 | RENCANA PLAFON ENTRANCE LT.01 ELV. +3.000 & ELV. +3.200 | | 50 |
| 51 | POTONGAN A & B | | 51 |
| 52 | ISOMETRY DETAIL PLAFON | | 52 |
| 53 | RENCANA PINTU & JENDELA LANTAI 01 | | 53 |
| 54 | RENCANA PINTU & JENDELA LANTAI 02 | | 54 |
| 55 | RENCANA PINTU & JENDELA LANTAI 03 | | 55 |
| 56 | RENCANA PINTU & JENDELA LANTAI 04 | | 56 |
| 57 | RENCANA PINTU & JENDELA LANTAI ATAP | | 57 |
| 58 | DETAIL PU01 | | 58 |
| 59 | DETAIL PU02 | | 59 |
| 60 | DETAIL PU02 | | 60 |
| 61 | DETAIL PU03 | | 61 |
| 62 | DETAIL P01 & P02 | | 62 |
| 63 | DETAIL P03 & P04 | | 63 |
| 64 | DETAIL P05 & P06 | | 64 |
| 65 | DETAIL P07 & P08 | | 65 |
| 66 | DETAIL P09 & PSH | | 66 |
| 67 | DETAIL P10 & P11 | | 67 |
| 68 | DETAIL P12 | | 68 |
| 69 | DETAIL J01 | | 69 |
| 70 | DETAIL J02 & J04 | | 70 |
| 71 | DETAIL J03 & J07 | | 71 |
| 72 | DETAIL J05 | | 72 |
| 73 | DETAIL J06 & J08 | | 73 |
| 74 | DETAIL J09 | | 74 |
| 75 | DETAIL BV01 & BV02 | | 75 |
| 76 | DETAIL BV03 & BV04 | | 76 |
| 77 | RENCANA PARTISI LANTAI 01 | | 77 |
| 78 | RENCANA PARTISI LANTAI 02 | | 78 |
| 79 | RENCANA PARTISI LANTAI 03 | | 79 |
| 80 | RENCANA PARTISI LANTAI 04 | | 80 |
| 81 | DETAIL PK01 | | 81 |
| 82 | DETAIL PK02 | | 82 |
| 83 | DETAIL PK03 | | 83 |
| 84 | DETAIL PR01 | | 84 |
| 85 | DETAIL PR02 & PR04 | | 85 |
| 86 | DETAIL PR03 | | 86 |
| 87 | DETAIL PR05 | | 87 |
| 88 | DETAIL PG01 | | 88 |
| 89 | DETAIL TRIBUN RUANG KONTROL | | 89 |
| 90 | DETAIL TRIBUN CINEMA | | 90 |
| 91 | DETAIL PANGGUNG DAN RANGKA VIDEOTRON | | 91 |
| 92 | RENCANA RAILING TANGGA UTAMA LT. 01 | | 92 |
| 93 | RENCANA RAILING TANGGA UTAMA LT. 02 | | 93 |
| 94 | RENCANA RAILING TANGGA UTAMA LT. 03 | | 94 |
| 95 | RENCANA RAILING TANGGA UTAMA LT. 04 | | 95 |
| 96 | DETAIL R01 & R02 | | 96 |
| 97 | DETAIL R03 & R04 | | 97 |
| 98 | DETAIL R05 & R06 | | 98 |
| 99 | RENCANA RAILING TIPE A LT. 01 - LT. 02 | | 99 |
| 100 | RENCANA RAILING TIPE A LT. 03 - LT. 04 | | 100 |

## DAFTAR ISI


| NO | JUDUL GAMBAR | KETERANGAN | NO. HAL |
|---|---|---|---|
| 101 | DETAIL R01 & R02 | | 101 |
| 102 | DETAIL R03 & R05 | | 102 |
| 103 | DETAIL R06 & R07 | | 103 |
| 104 | RENCANA RAILING TIPE B LT. 01 - LT. 02 | | 104 |
| 105 | RENCANA RAILING TIPE B LT. 03 - LT. 04 | | 105 |
| 106 | DETAIL R01 & R02 | | 106 |
| 107 | DETAIL R03 & R05 | | 107 |
| 108 | DETAIL R06 & R07 | | 108 |
| 109 | RENCANA RAILING TIPE C LT. 04 - LT. ATAP | | 109 |
| 110 | DETAIL R01 - R03 | | 110 |
| 111 | DETAIL RAILING RAMP DIFABEL | | 111 |
| 112 | DENAH TOILET TIPE A LT. 01 - LT. 04 | | 112 |
| 113 | POTONGAN A | | 113 |
| 114 | POTONGAN B | | 114 |
| 115 | POTONGAN C | | 115 |
| 116 | POTONGAN D | | 116 |
| 117 | DENAH TOILET TIPE B LT. 02 - LT. 04 | | 117 |
| 118 | POTONGAN A | | 118 |
| 119 | POTONGAN B | | 119 |
| 120 | POTONGAN C | | 120 |
| 121 | POTONGAN D | | 121 |
| 122 | DENAH TOILET TIPE C LT. 01 | | 122 |
| 123 | POTONGAN A & POTONGAN B | | 123 |
| 124 | POTONGAN C & POTONGAN D | | 124 |
| 125 | DETAIL - DETAIL | | 125 |
| 126 | DETAIL - DETAIL SANITAIR | | 126 |
| 127 | RENCANA DETAIL TAMPAK A | | 127 |
| 128 | RENCANA DETAIL TAMPAK B | | 128 |
| 129 | RENCANA DETAIL TAMPAK C | | 129 |
| 130 | RENCANA DETAIL TAMPAK D | | 130 |
| 131 | DETAIL 01 | | 131 |
| 132 | DETAIL 02 | | 132 |
| 133 | DETAIL IDENTITAS GEDUNG | | 133 |
| 134 | DETAIL 03 | | 134 |
| 135 | DETAIL 04 | | 135 |
| 136 | DETAIL 05 | | 136 |
| 137 | DETAIL 06 | | 137 |
| 138 | DETAIL COVER KOLOM | | 138 |
| 139 | DETAIL - DETAIL BALOK PRAKTIS | | 139 |
| 140 | DETAIL - DETAIL KOLOM & BALOK PRAKTIS | | 140 |
| | POTONGAN KOLOM & BALOK PRAKTIS | | |
| 141 | RENCANA KOLOM PRAKTIS LANTAI 01 | | 141 |
| 142 | RENCANA KOLOM PRAKTIS LANTAI 02 | | 142 |
| 143 | RENCANA KOLOM PRAKTIS LANTAI 03 | | 143 |
| 144 | RENCANA KOLOM PRAKTIS LANTAI 04 | | 144 |
| 145 | RENCANA KOLOM PRAKTIS LANTAI ATAP | | 145 |
| 146 | RENCANA BALOK PRAKTIS LANTAI 01 | | 146 |
| 147 | RENCANA BALOK PRAKTIS LANTAI 02 | | 147 |
| 148 | RENCANA BALOK PRAKTIS LANTAI 03 | | 148 |
| 149 | RENCANA BALOK PRAKTIS LANTAI 04 | | 149 |

| NO | JUDUL GAMBAR | KETERANGAN | NO. HAL |
|---|---|---|---|
| 150 | RENCANA BALOK PRAKTIS LT ATAP | | 150 |
| 151 | RENCANA BALOK LATEIU LT 01 ELV. (+0.400) - (+1.200) | | 151 |
| 152 | RENCANA BALOK LATEIU LT 01 ELV. (+1.600) - (+2.400) | | 152 |
| 153 | RENCANA BALOK LATEIU LT 01 ELV. (+2.800) | | 153 |
| 154 | RENCANA BALOK LATEIU LT 02 ELV. (+4.600) - (+5.400) | | 154 |
| 155 | RENCANA BALOK LATEIU LT 02 ELV. (+5.800) - (+6.600) | | 155 |
| 156 | RENCANA BALOK LATEIU LT 02 ELV. +7.000 | | 156 |
| 157 | RENCANA BALOK LATEIU LT 03 ELV. (+8.800) - (+9.600) | | 157 |
| 158 | RENCANA BALOK LATEIU LT 03 ELV. (+10.000) - (+10.800) | | 158 |
| 159 | RENCANA BALOK LATEIU LT 03 ELV. +11.200 | | 159 |
| 160 | RENCANA BALOK LATEIU LT 04 ELV. (+13.000) - (+13.800) | | 160 |
| 161 | RENCANA BALOK LATEIU LT 04 ELV. (+14.200) - (+15.000) | | 161 |
| 162 | RENCANA BALOK LATEIU LT 04 ELV. +15.400 | | 162 |

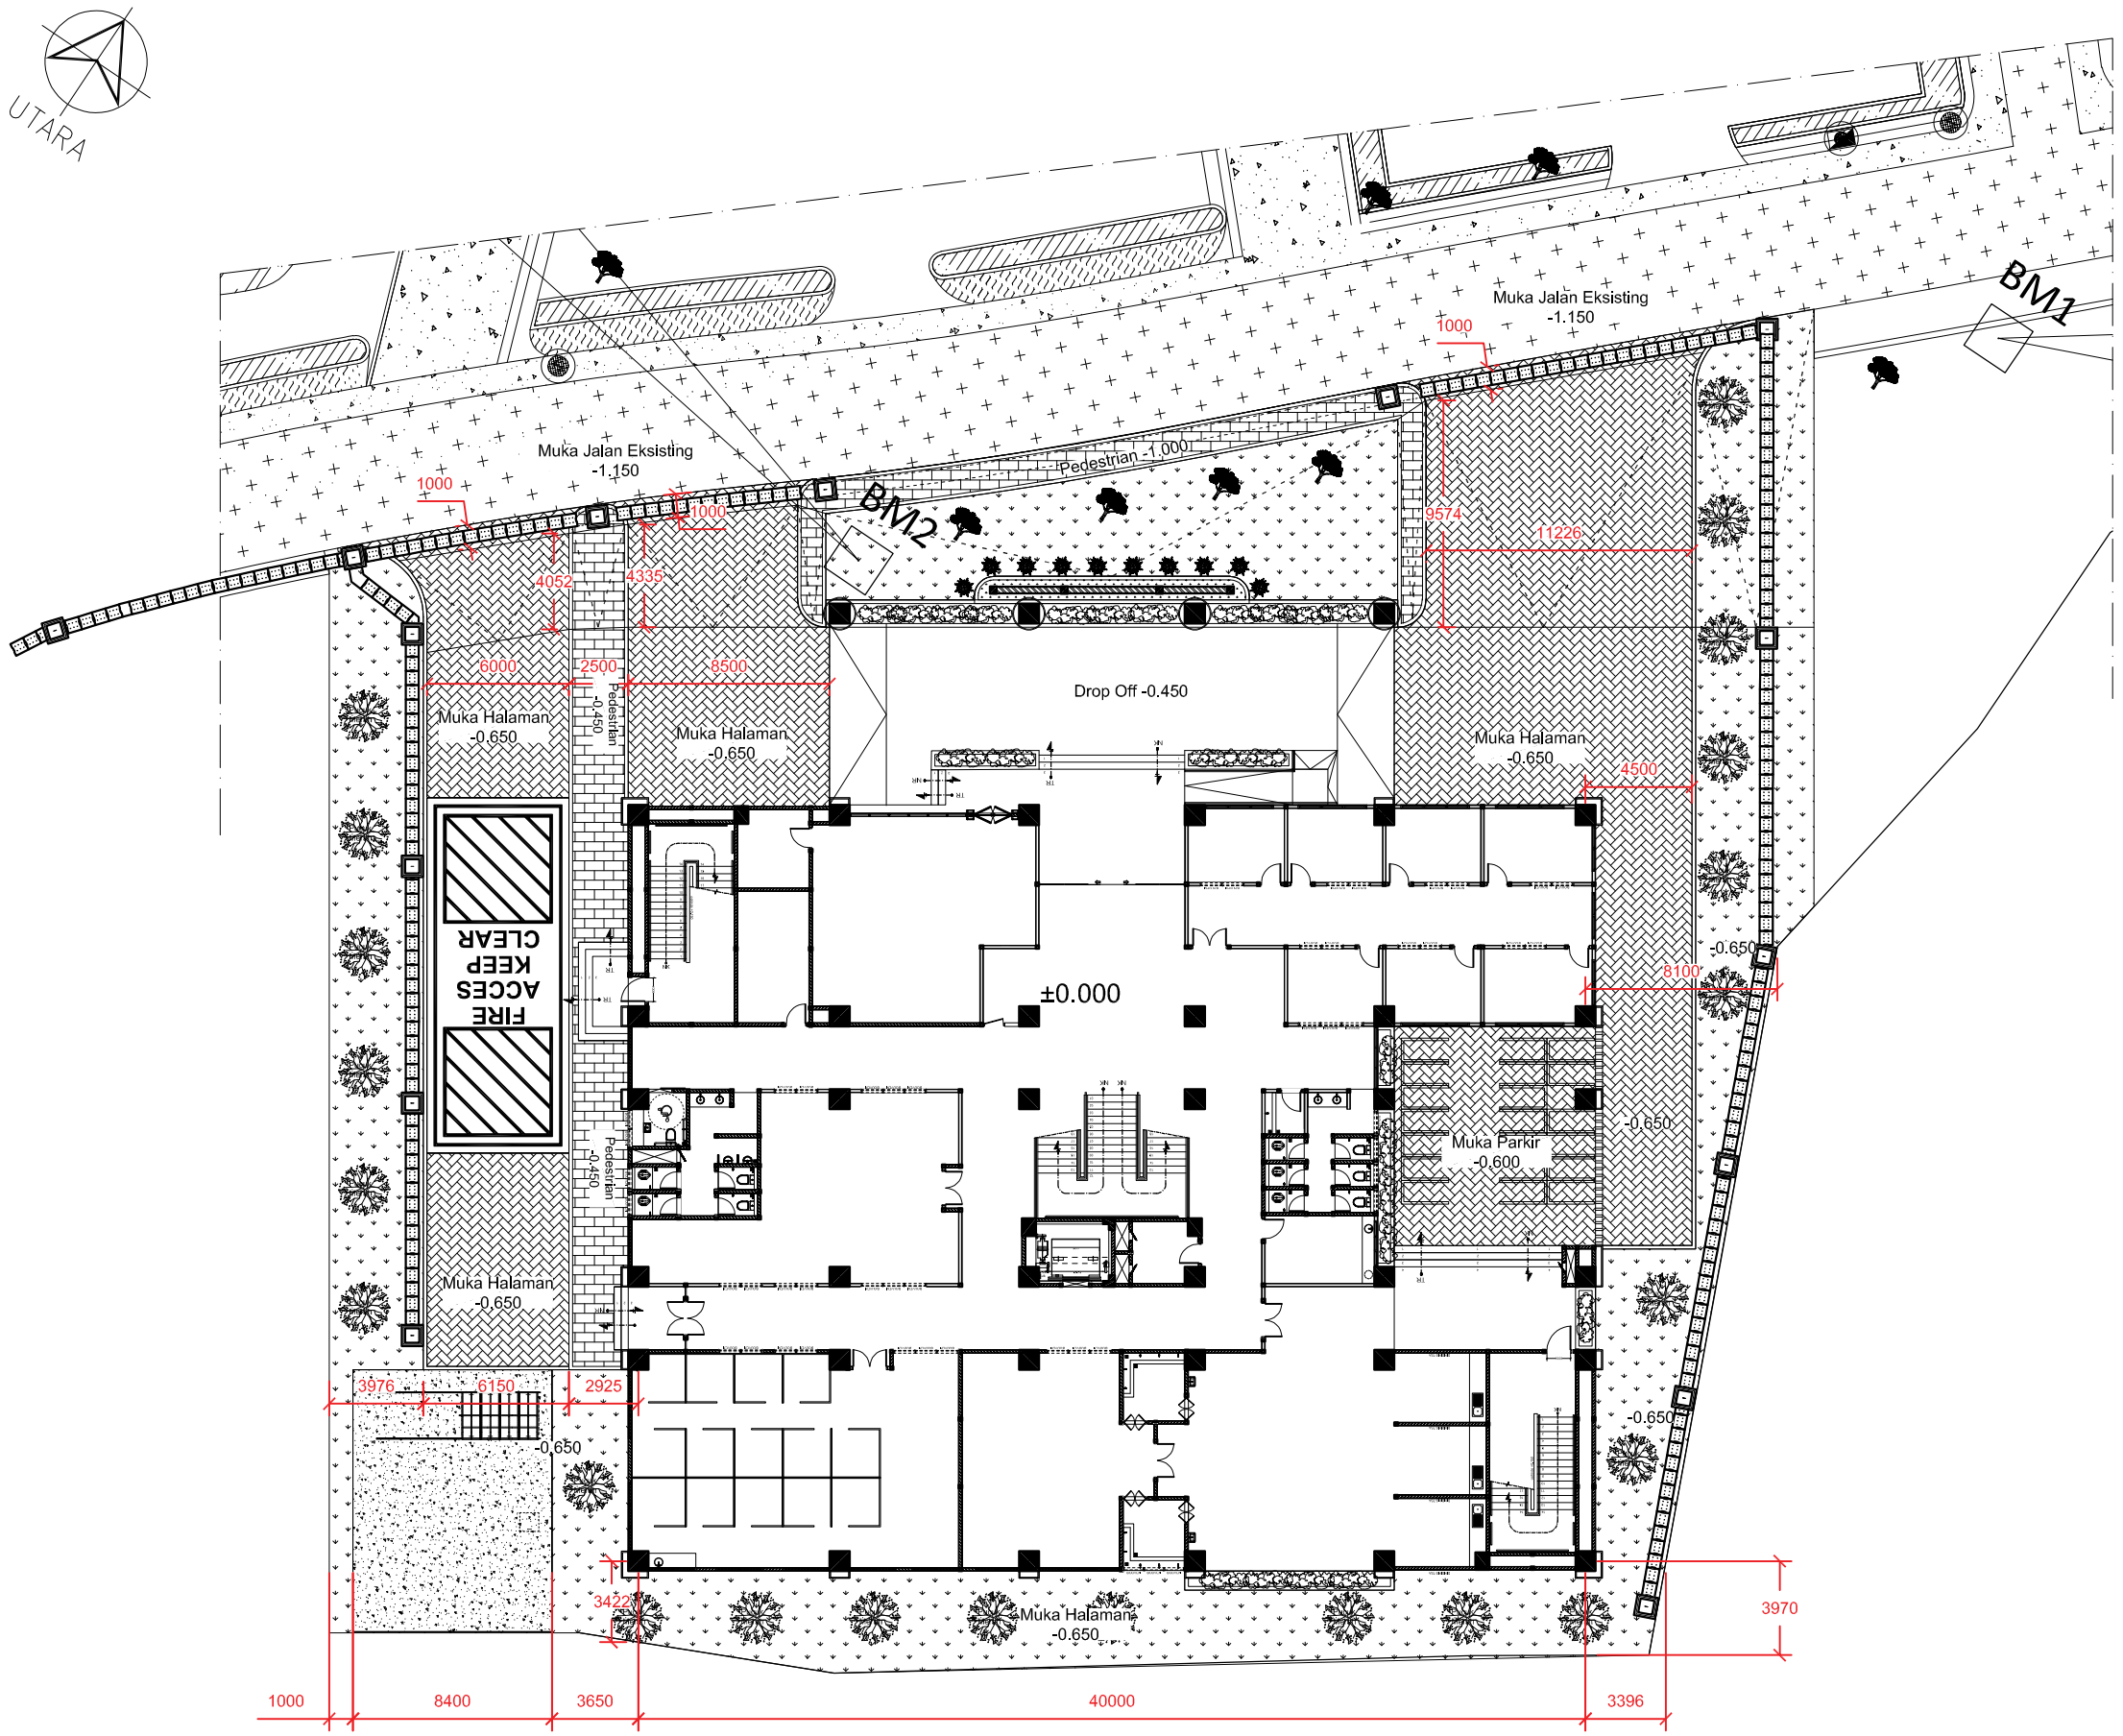


**SITE PLAN**
SKALA 1 : 300

UIN
SJECH M. DJAMIL DJAMBEK
BUKITTINGGI

KEMENTERIAN AGAMA REPUBLIK INDONESIA
**UNIVERSITAS ISLAM NEGERI**
**SJECH M. DJAMIL DJAMBEK**
JL. GURUN AUR KUBANG PUTIH, KABUPATEN AGAM, SUMATERA BARAT

**PEKERJAAN**

**PEMBANGUNAN GEDUNG PENDIDIKAN TERPADU**

**LOKASI**


**JL. GURUN AUR, KENAGARIAN KUBANG PUTIAH, KECAMATAN BANUHAMPU, KABUPATEN AGAM, SUMATERA BARAT**

**TAHUN ANGGARAN**

**2026**

| JUDUL GAMBAR | SKALA |
|---|---|
| SITE PLAN | 1 : 300 |

| KODE | NO. LBR | JML. LBR |
|---|---|---|
| ARS | 1 | 162 |

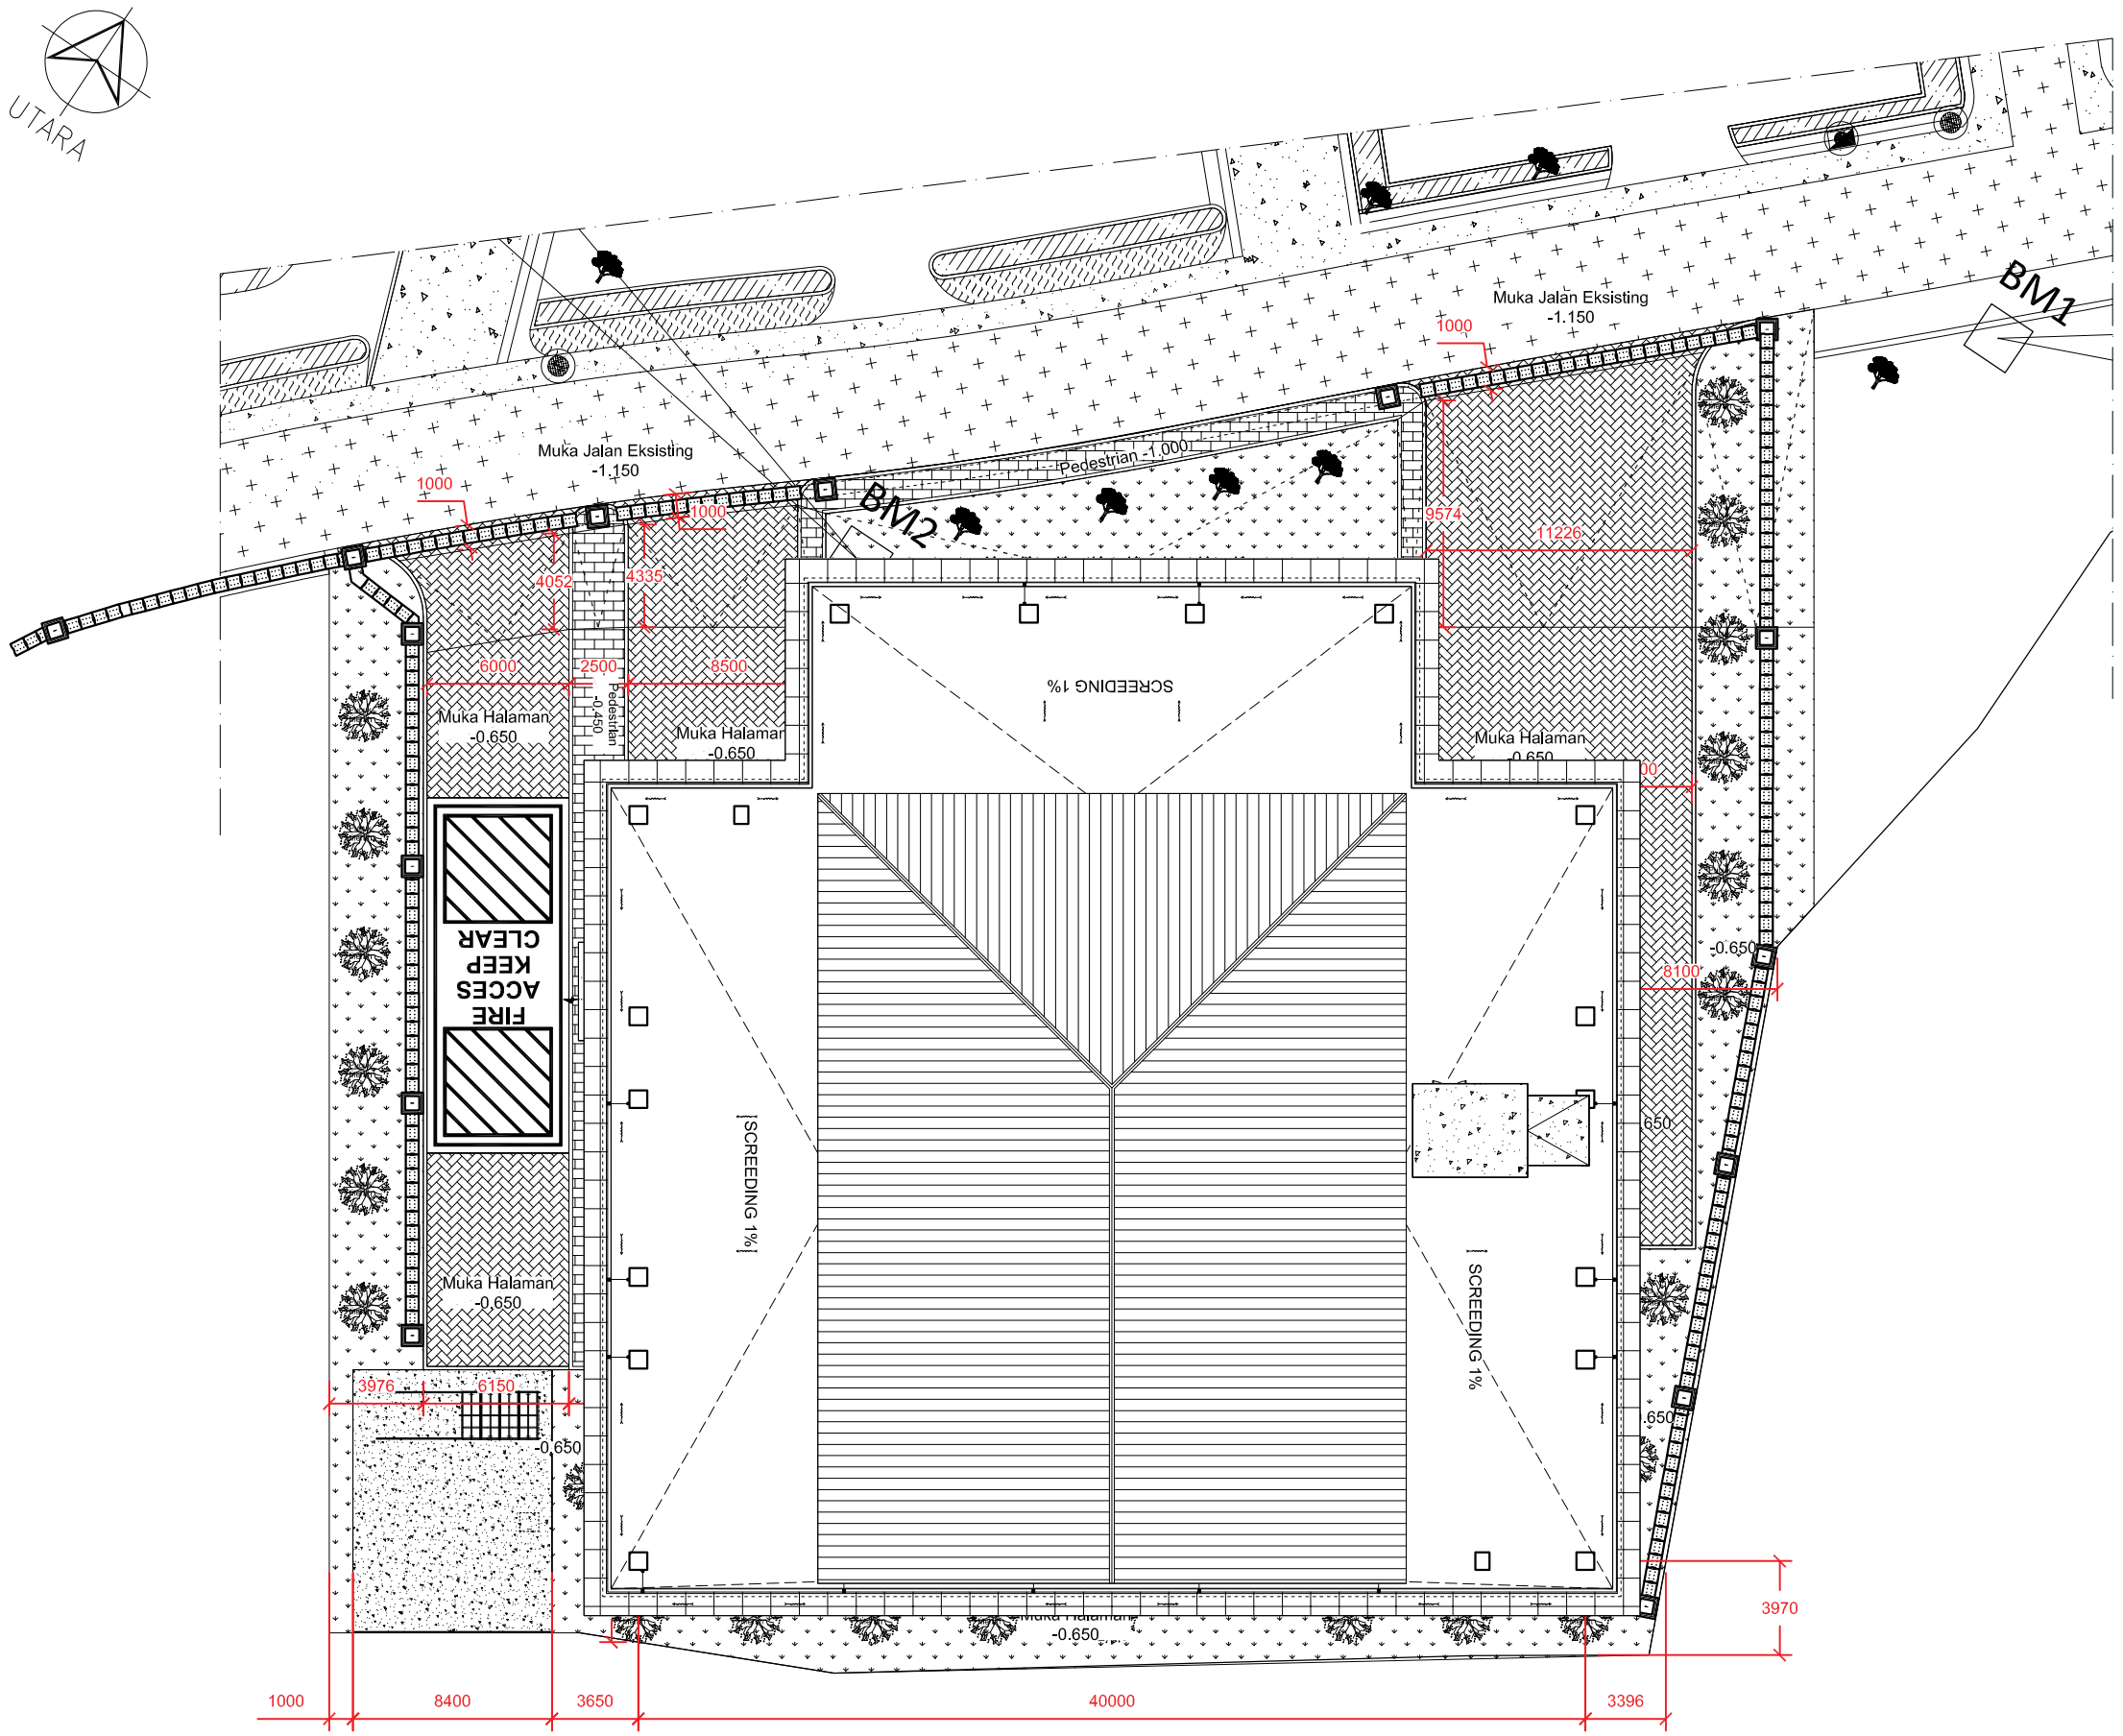


**SITE SITUASI**
SKALA 1 : 300

UIN
SJECH M. DJAMIL DJAMBEK
BUKITTINGGI

KEMENTERIAN AGAMA REPUBLIK INDONESIA
**UNIVERSITAS ISLAM NEGERI**
**SJECH M. DJAMIL DJAMBEK**
JL. GURUN AUR KUBANG PUTIH, KABUPATEN AGAM, SUMATERA BARAT

**PEKERJAAN**

**PEMBANGUNAN GEDUNG PENDIDIKAN TERPADU**

**LOKASI**


**JL. GURUN AUR, KENAGARIAN KUBANG PUTIAH, KECAMATAN BANUHAMPU, KABUPATEN AGAM, SUMATERA BARAT**

**TAHUN ANGGARAN**


**2026**

| JUDUL GAMBAR | SKALA |
|---|---|
| SITE SITUASI | 1 : 300 |

| KODE | NO. LBR | JML. LBR |
|---|---|---|
| ARS | 2 | 162 |

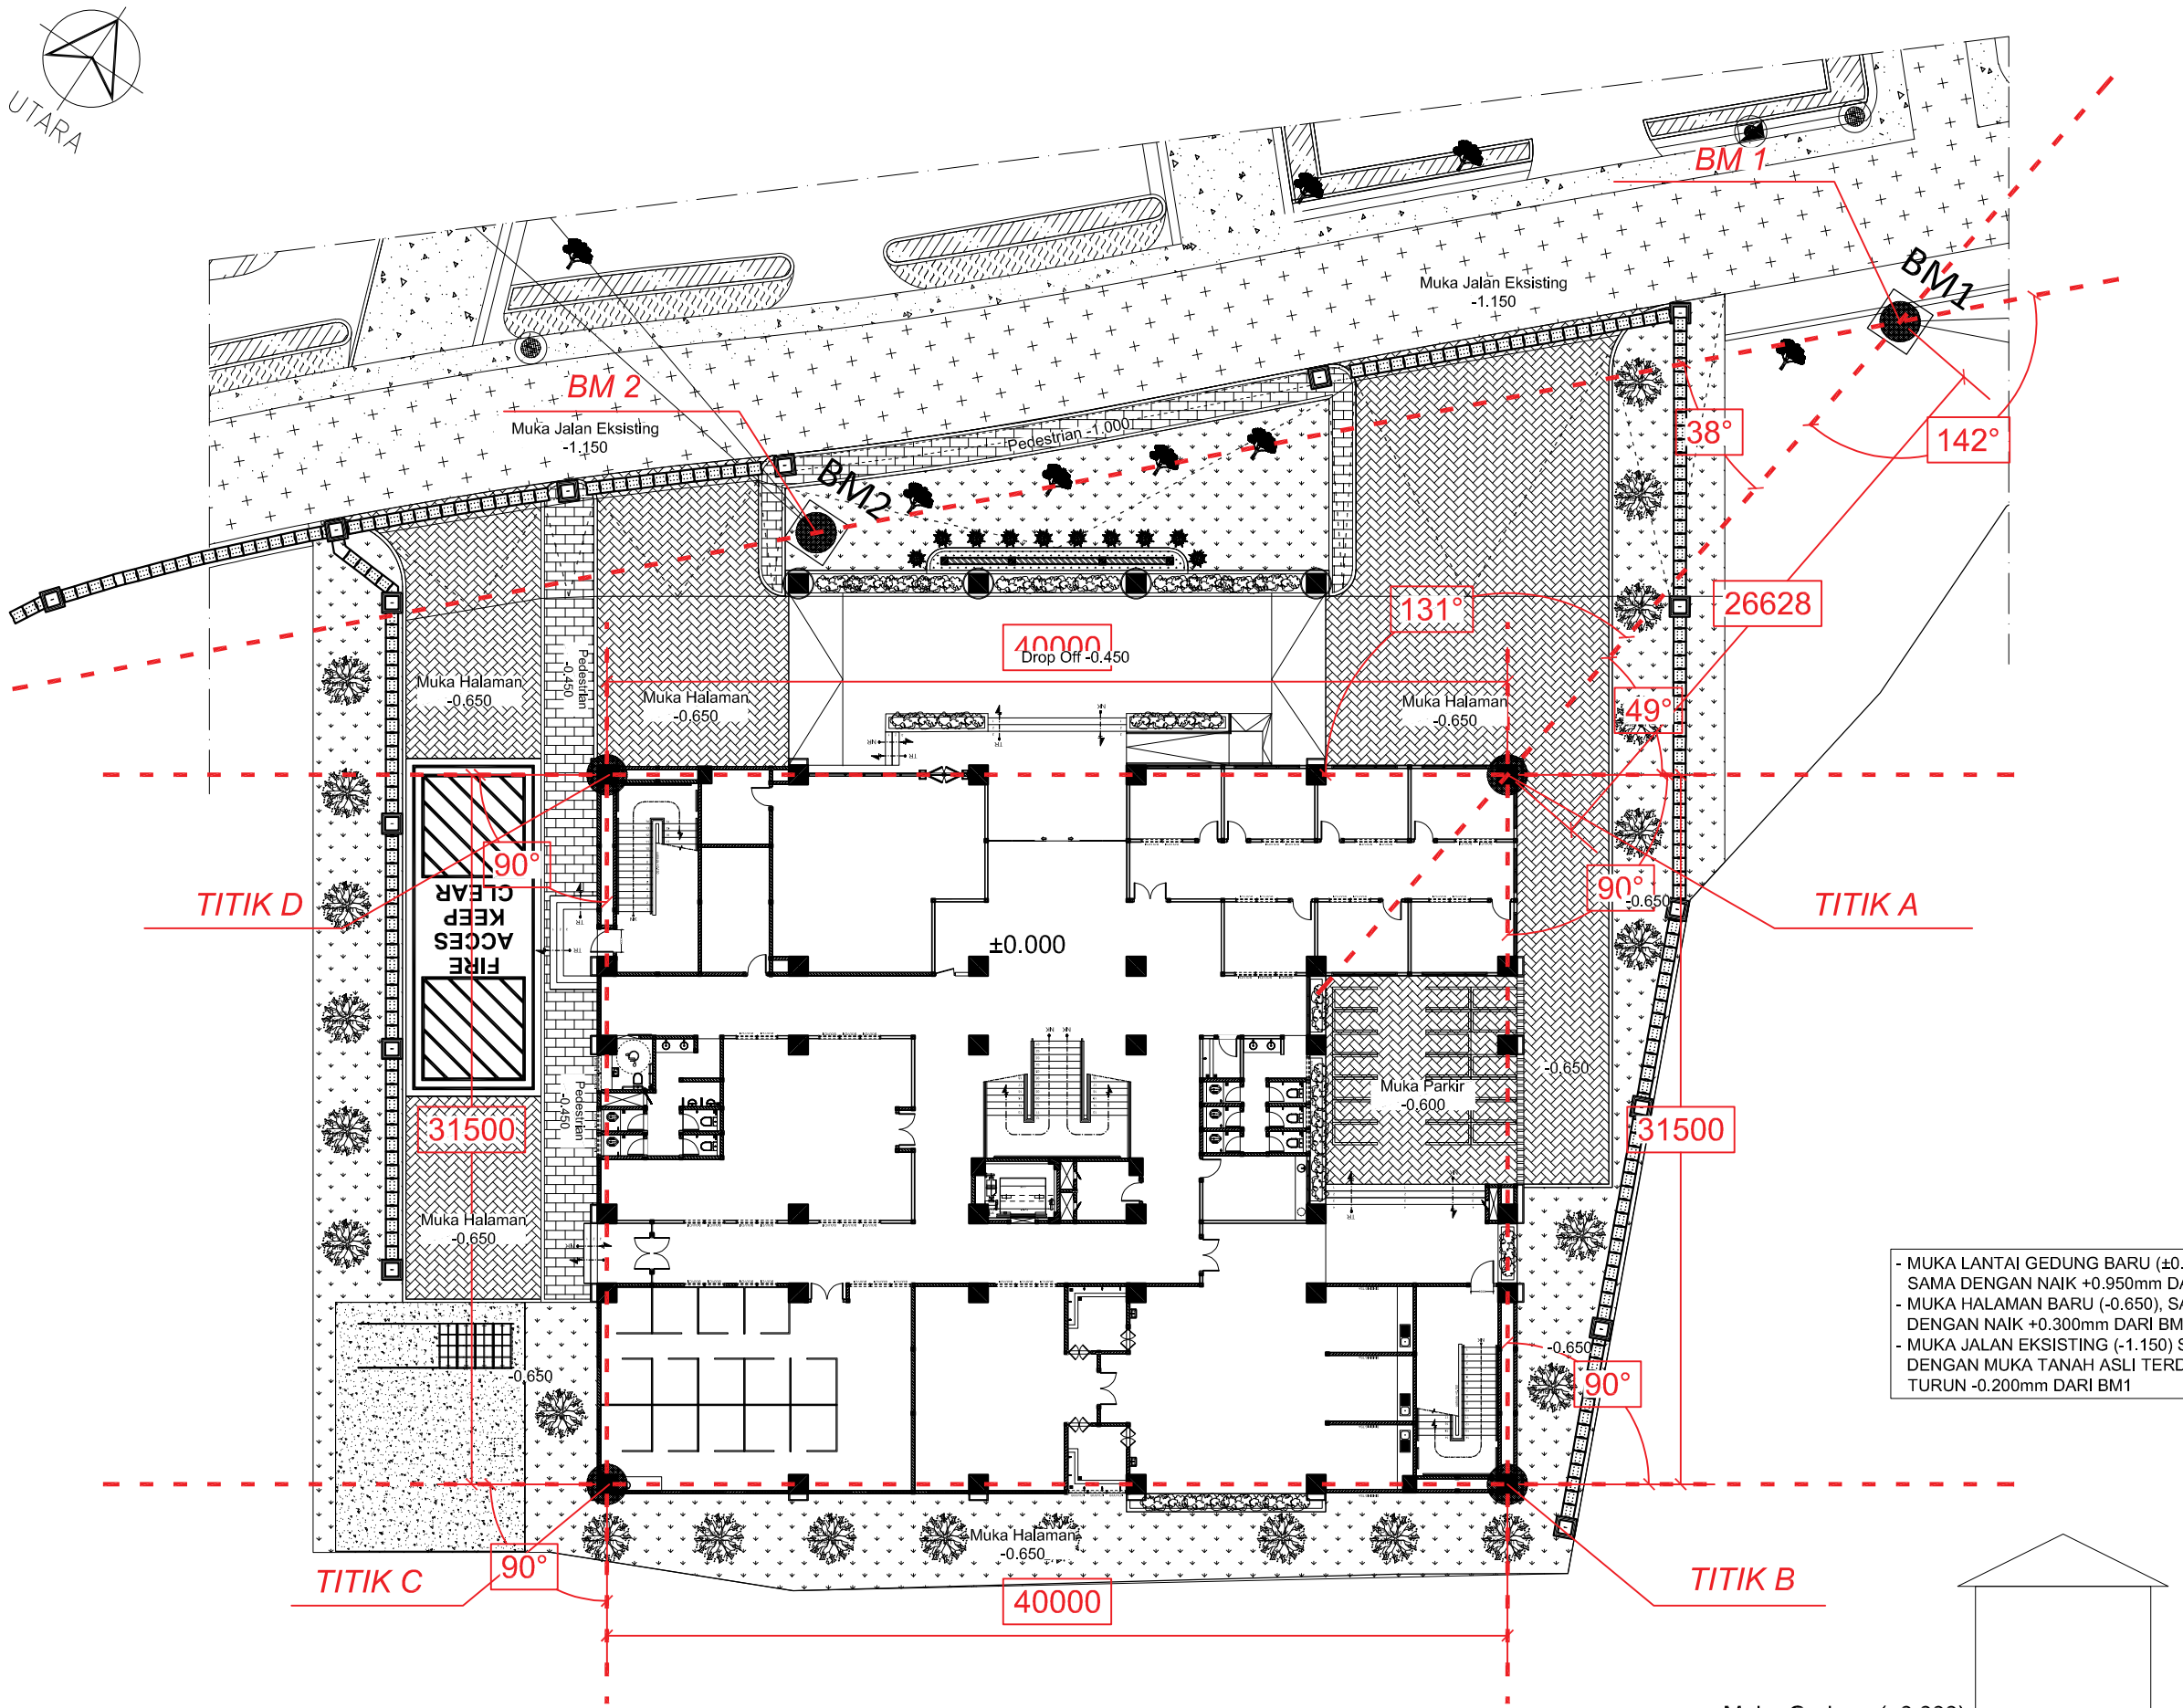


- MUKA LANTAI GEDUNG BARU (±0.000), SAMA DENGAN NAIK +0.950mm DARI BM1
- MUKA HALAMAN BARU (-0.650), SAMA DENGAN NAIK +0.300mm DARI BM1
- MUKA JALAN EKSISTING (-1.150) SAMA DENGAN MUKA TANAH ASLI TERDALAM, TURUN -0.200mm DARI BM1

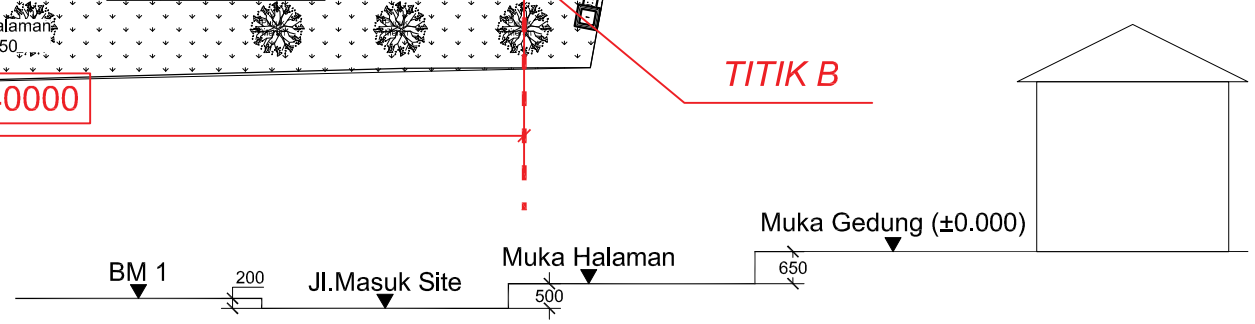


**Skematik Pengambilan elevasi**

**RENCANA PENGAMBILAN SIKU BANGUNAN**
SKALA 1 : 300


UIN
SJECH M. DJAMIL DJAMBEK
BUKITTINGGI

KEMENTERIAN AGAMA REPUBLIK INDONESIA
UNIVERSITAS ISLAM NEGERI
SJECH M. DJAMIL DJAMBEK
JL. GURUN AUR KUBANG PUTIH, KABUPATEN AGAM, SUMATERA BARAT


**PEKERJAAN**

PEMBANGUNAN GEDUNG PENDIDIKAN TERPADU

**LOKASI**


JL. GURUN AUR, KENAGARIAN KUBANG PUTIAH, KECAMATAN BANUHAMPU, KABUPATEN AGAM, SUMATERA BARAT

**TAHUN ANGGARAN**

2026

| JUDUL GAMBAR | SKALA |
|---|---|
| RENCANA PENGAMBILAN SIKU BANGUNAN | 1 : 300 |

| KODE | NO. LBR | JML. LBR |
|---|---|---|
| ARS | 3 | 162 |

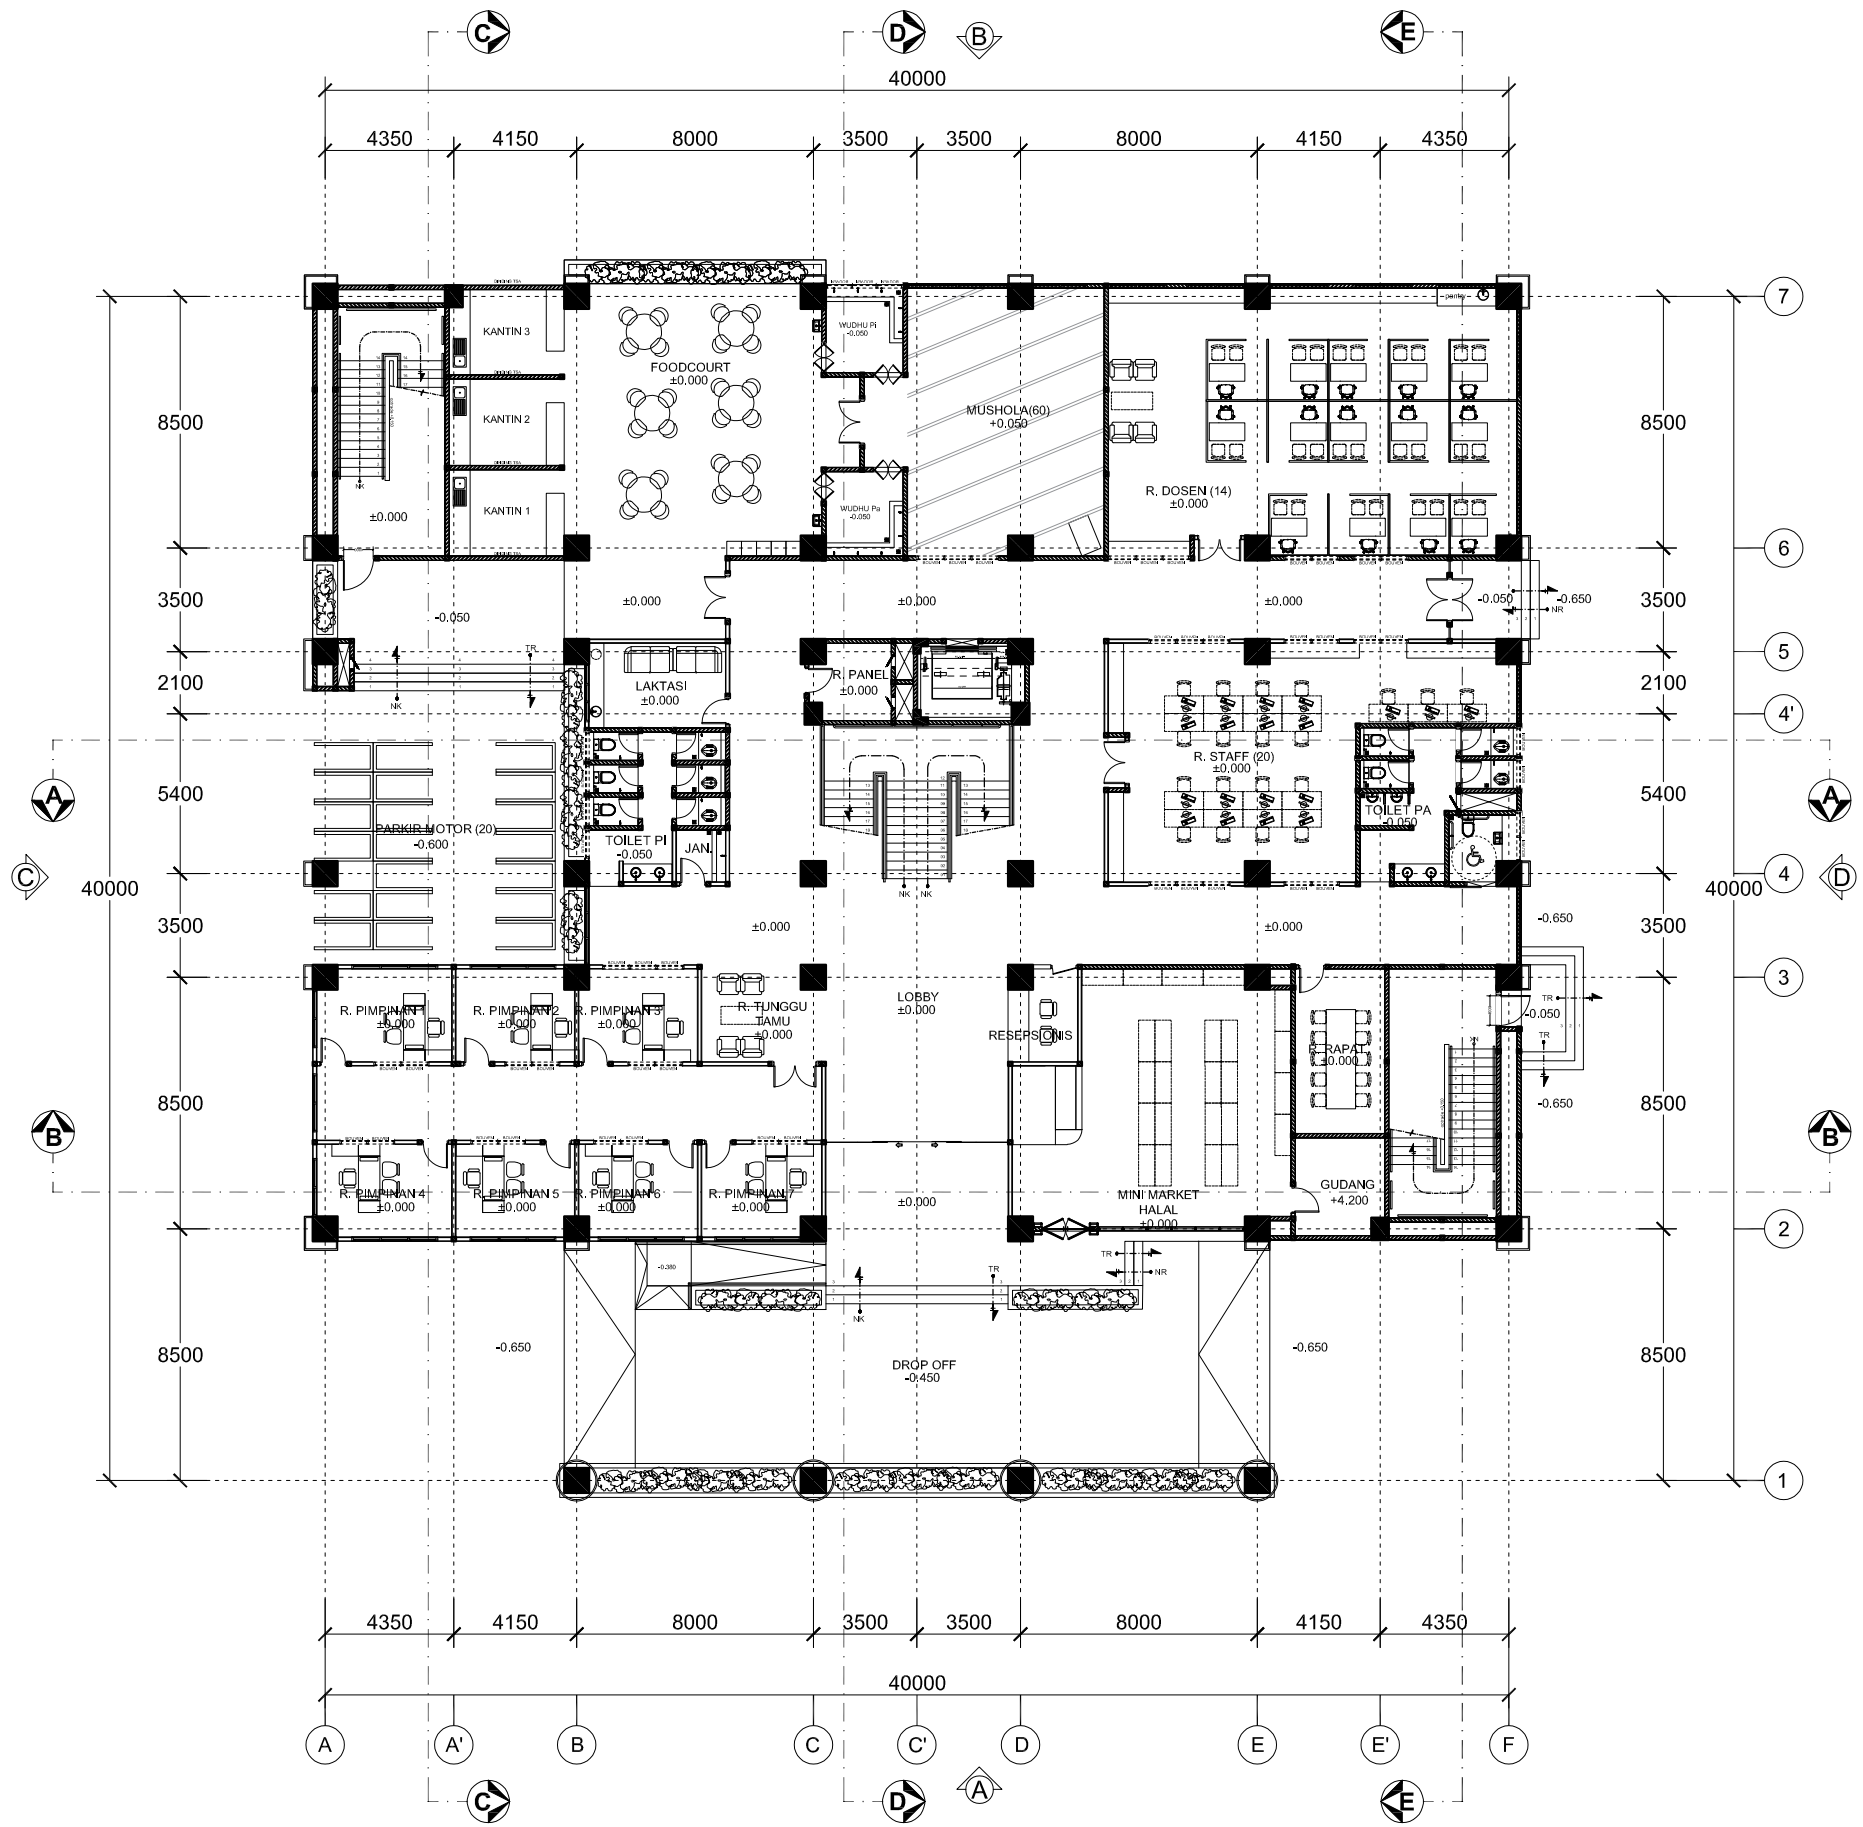


## DENAH LANTAI 01

SKALA 1 : 250


UIN
SJECH M. DJAMIL DJAMBEK
BUKITTINGGI

KEMENTERIAN AGAMA REPUBLIK INDONESIA
**UNIVERSITAS ISLAM NEGERI**
**SJECH M. DJAMIL DJAMBEK**
JL. GURUN AUR KUBANG PUTIH, KABUPATEN AGAM, SUMATERA BARAT


**PEKERJAAN**

PEMBANGUNAN GEDUNG PENDIDIKAN TERPADU

**LOKASI**


JL. GURUN AUR, KENAGARIAN KUBANG PUTIAH, KECAMATAN BANUHAMPU, KABUPATEN AGAM, SUMATERA BARAT

**TAHUN ANGGARAN**

2026

| JUDUL GAMBAR | SKALA |
|---|---|
| DENAH LANTAI 01 | 1 : 250 |

| KODE | NO. LBR | JML. LBR |
|---|---|---|
| ARS | 4 | 162 |

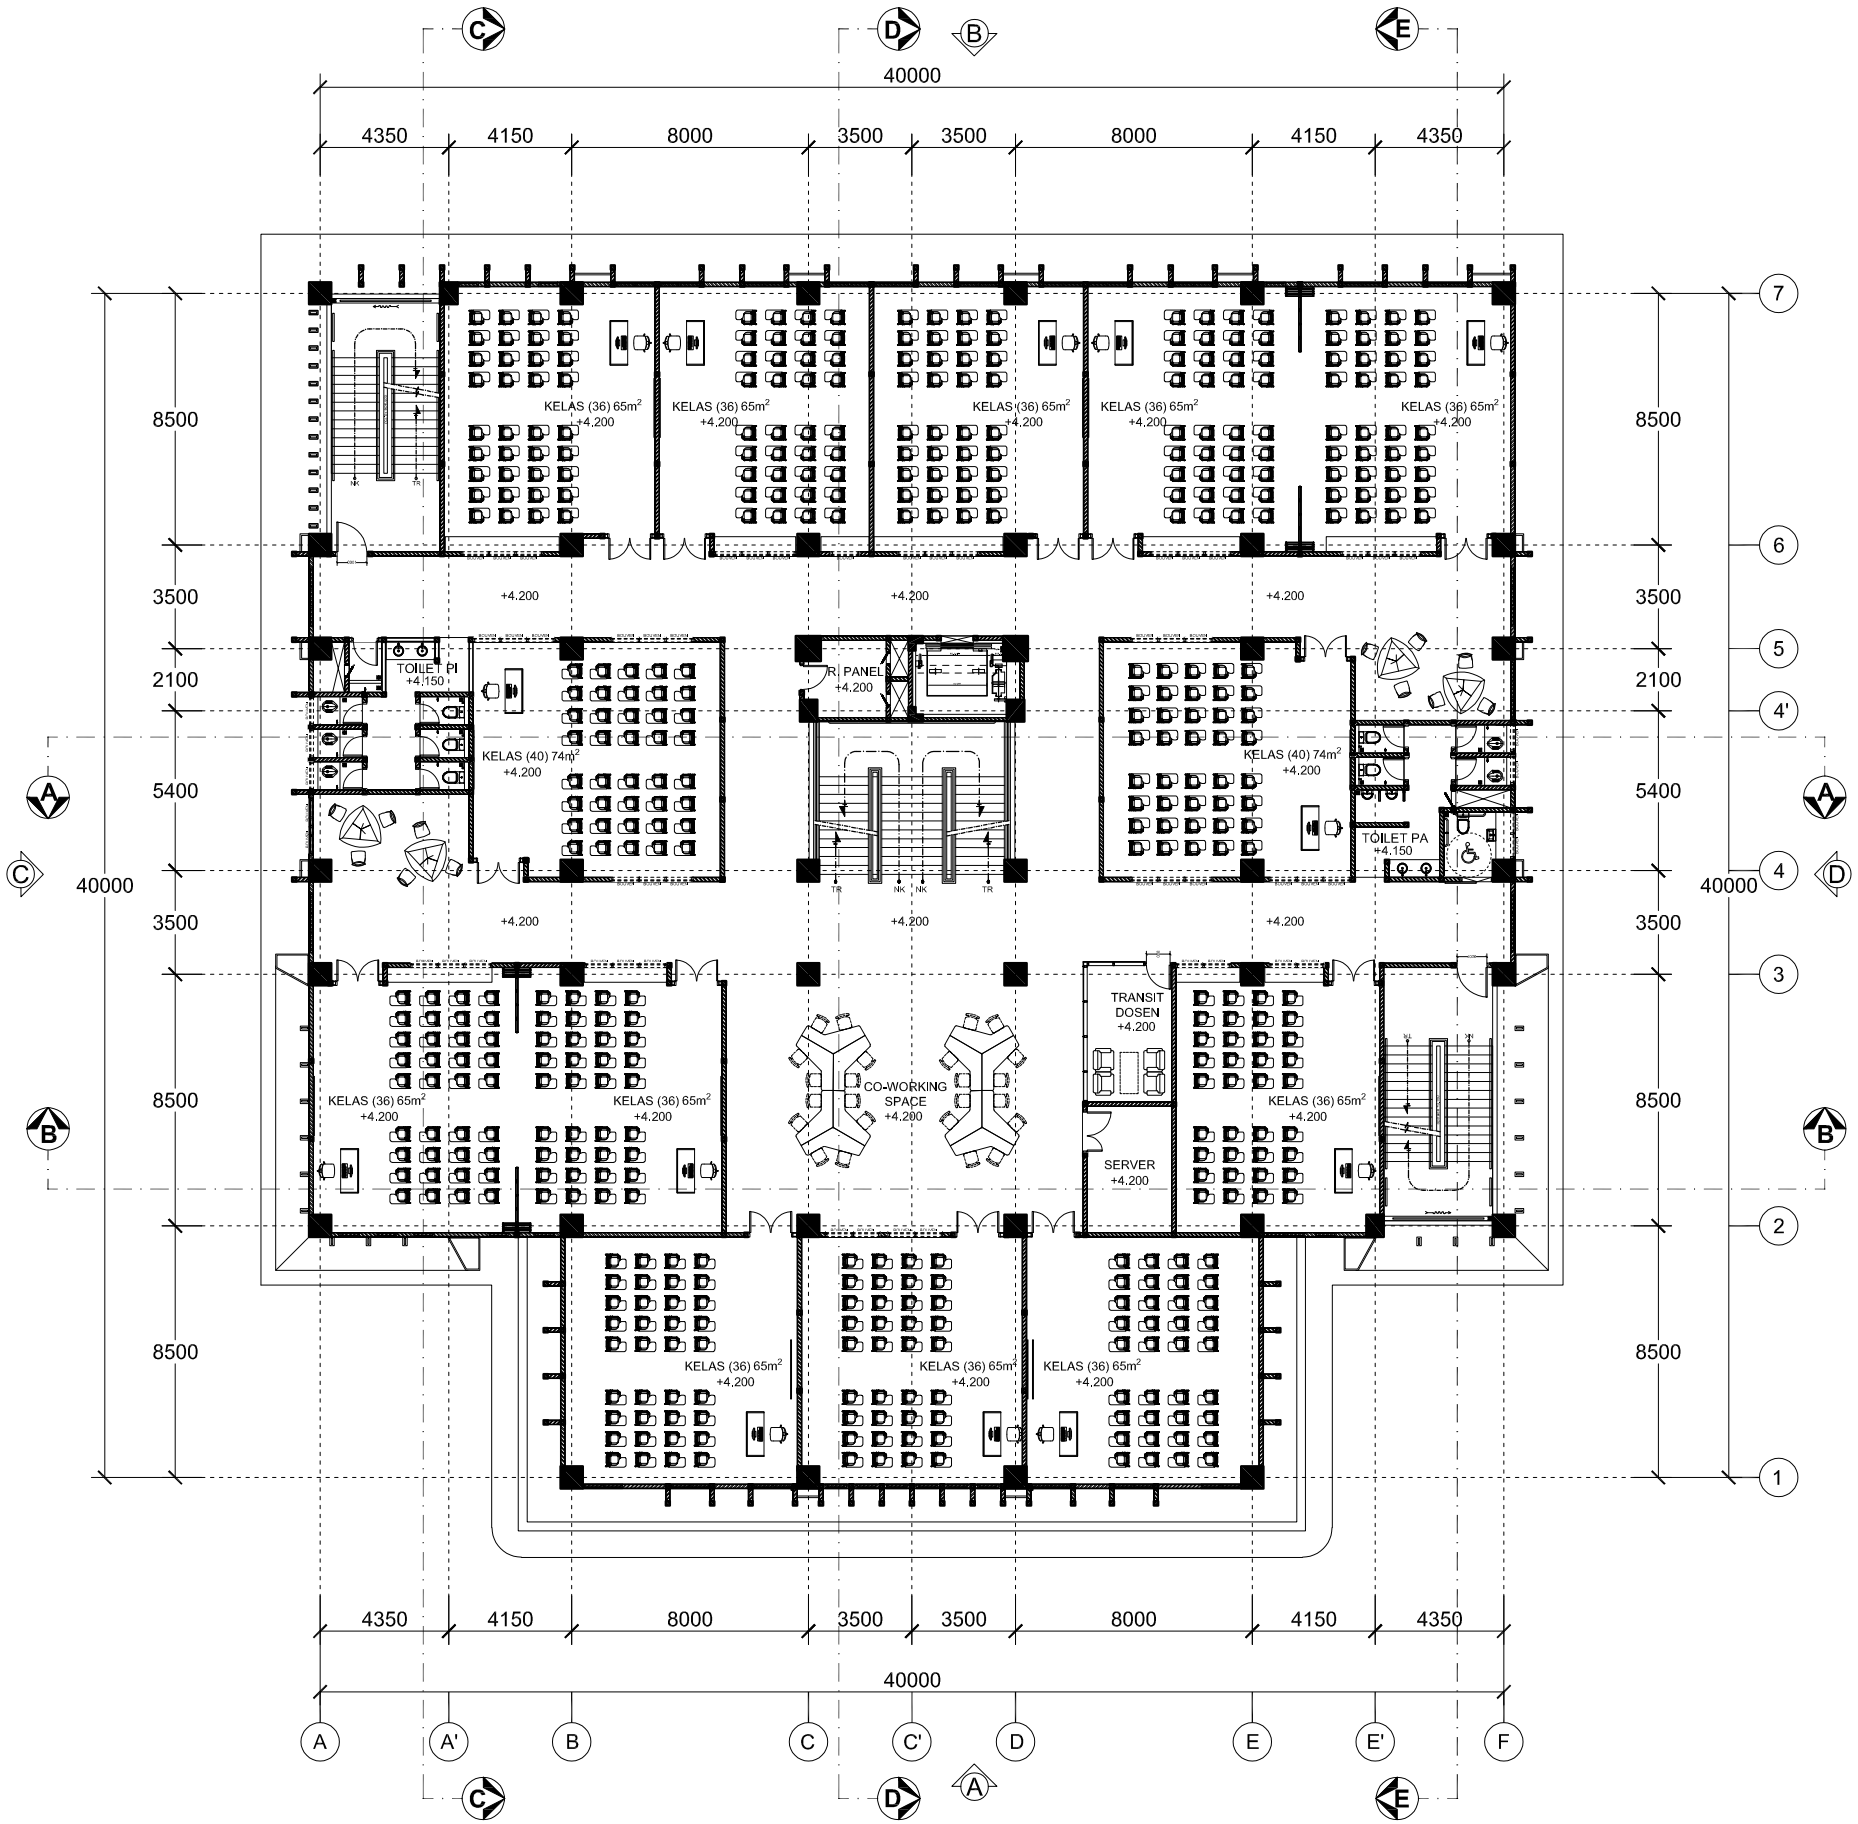


# DENAH LANTAI 02

SKALA 1 : 250


KEMENTERIAN AGAMA REPUBLIK INDONESIA
**UNIVERSITAS ISLAM NEGERI**
**SJECH M. DJAMIL DJAMBEK**
JL. GURUN AUR KUBANG PUTIH, KABUPATEN AGAM, SUMATERA BARAT


**PEKERJAAN**

**PEMBANGUNAN GEDUNG PENDIDIKAN TERPADU**

**LOKASI**


**JL. GURUN AUR, KENAGARIAN KUBANG PUTIAH, KECAMATAN BANUHAMPU, KABUPATEN AGAM, SUMATERA BARAT**

**TAHUN ANGGARAN**

**2026**

| JUDUL GAMBAR | SKALA |
|---|---|
| DENAH LANTAI 02 | 1 : 250 |

| KODE | NO. LBR | JML. LBR |
|---|---|---|
| ARS | 5 | 162 |

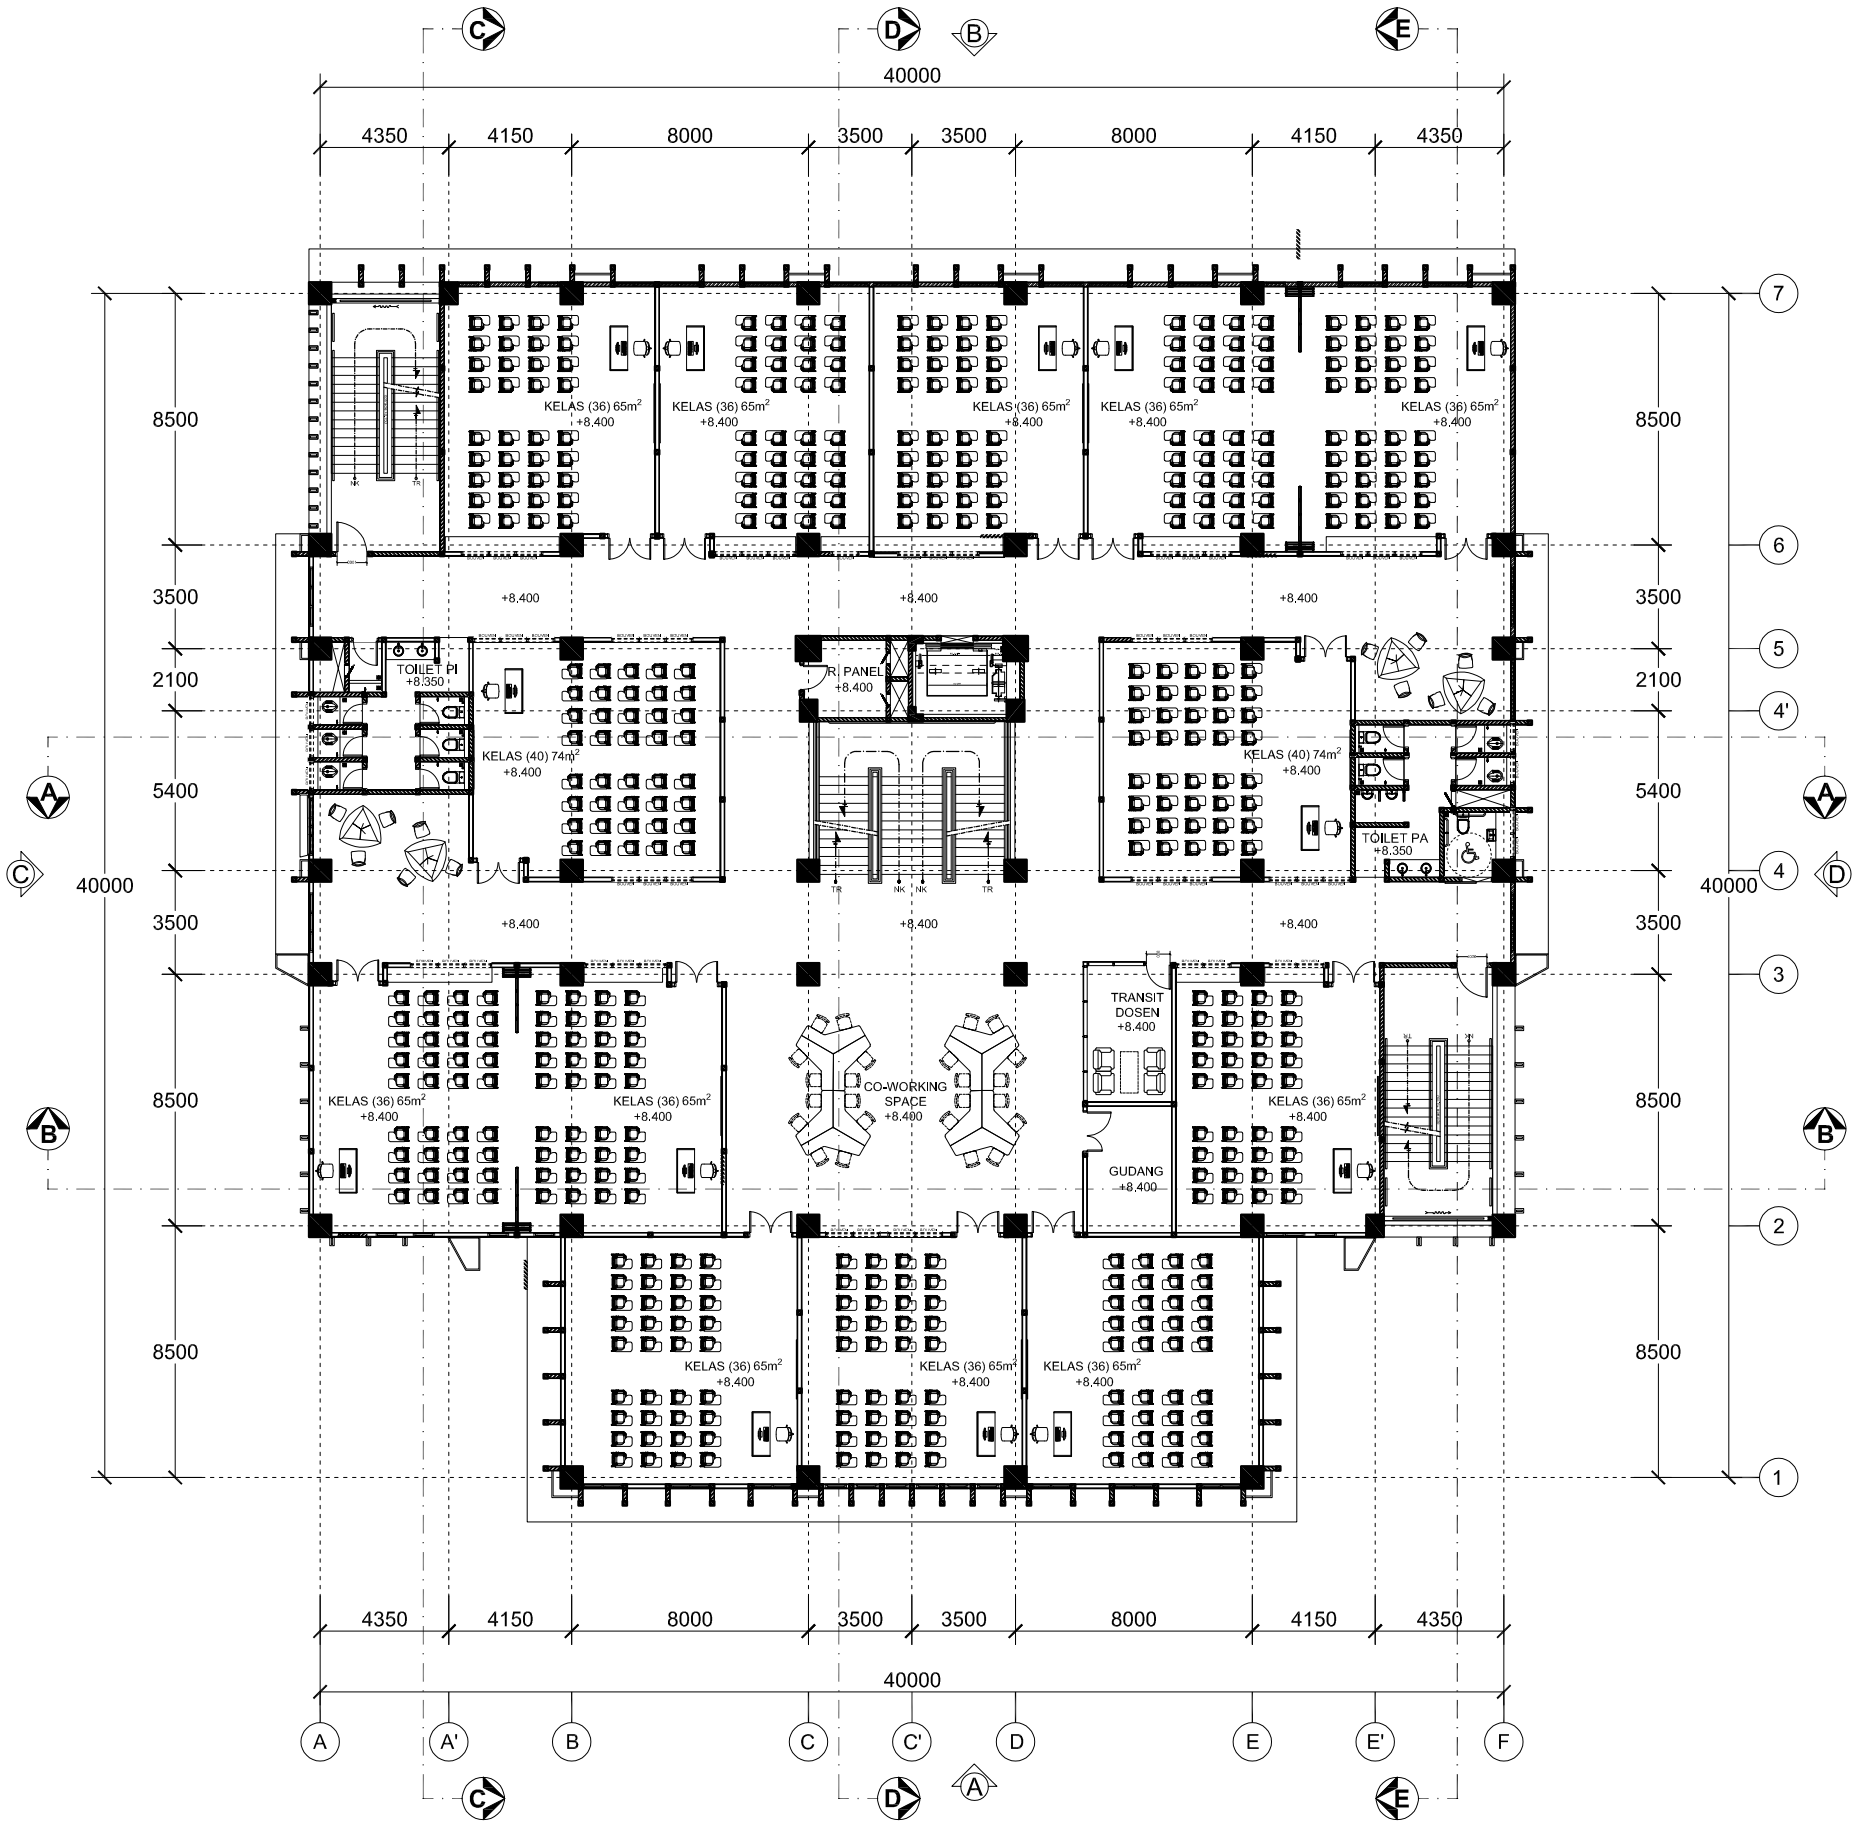


# DENAH LANTAI 03

SKALA 1 : 250

UIN
SJECH M. DJAMIL DJAMBEK
BUKITTINGGI

KEMENTERIAN AGAMA REPUBLIK INDONESIA
**UNIVERSITAS ISLAM NEGERI**
**SJECH M. DJAMIL DJAMBEK**
JL. GURUN AUR KUBANG PUTIH, KABUPATEN AGAM, SUMATERA BARAT

**PEKERJAAN**

**PEMBANGUNAN GEDUNG PENDIDIKAN TERPADU**

**LOKASI**


**JL. GURUN AUR, KENAGARIAN KUBANG PUTIAH, KECAMATAN BANUHAMPU, KABUPATEN AGAM, SUMATERA BARAT**

**TAHUN ANGGARAN**

**2026**

| JUDUL GAMBAR | SKALA |
|---|---|
| DENAH LANTAI 03 | 1 : 250 |

| KODE | NO. LBR | JML. LBR |
|---|---|---|
| ARS | 6 | 162 |

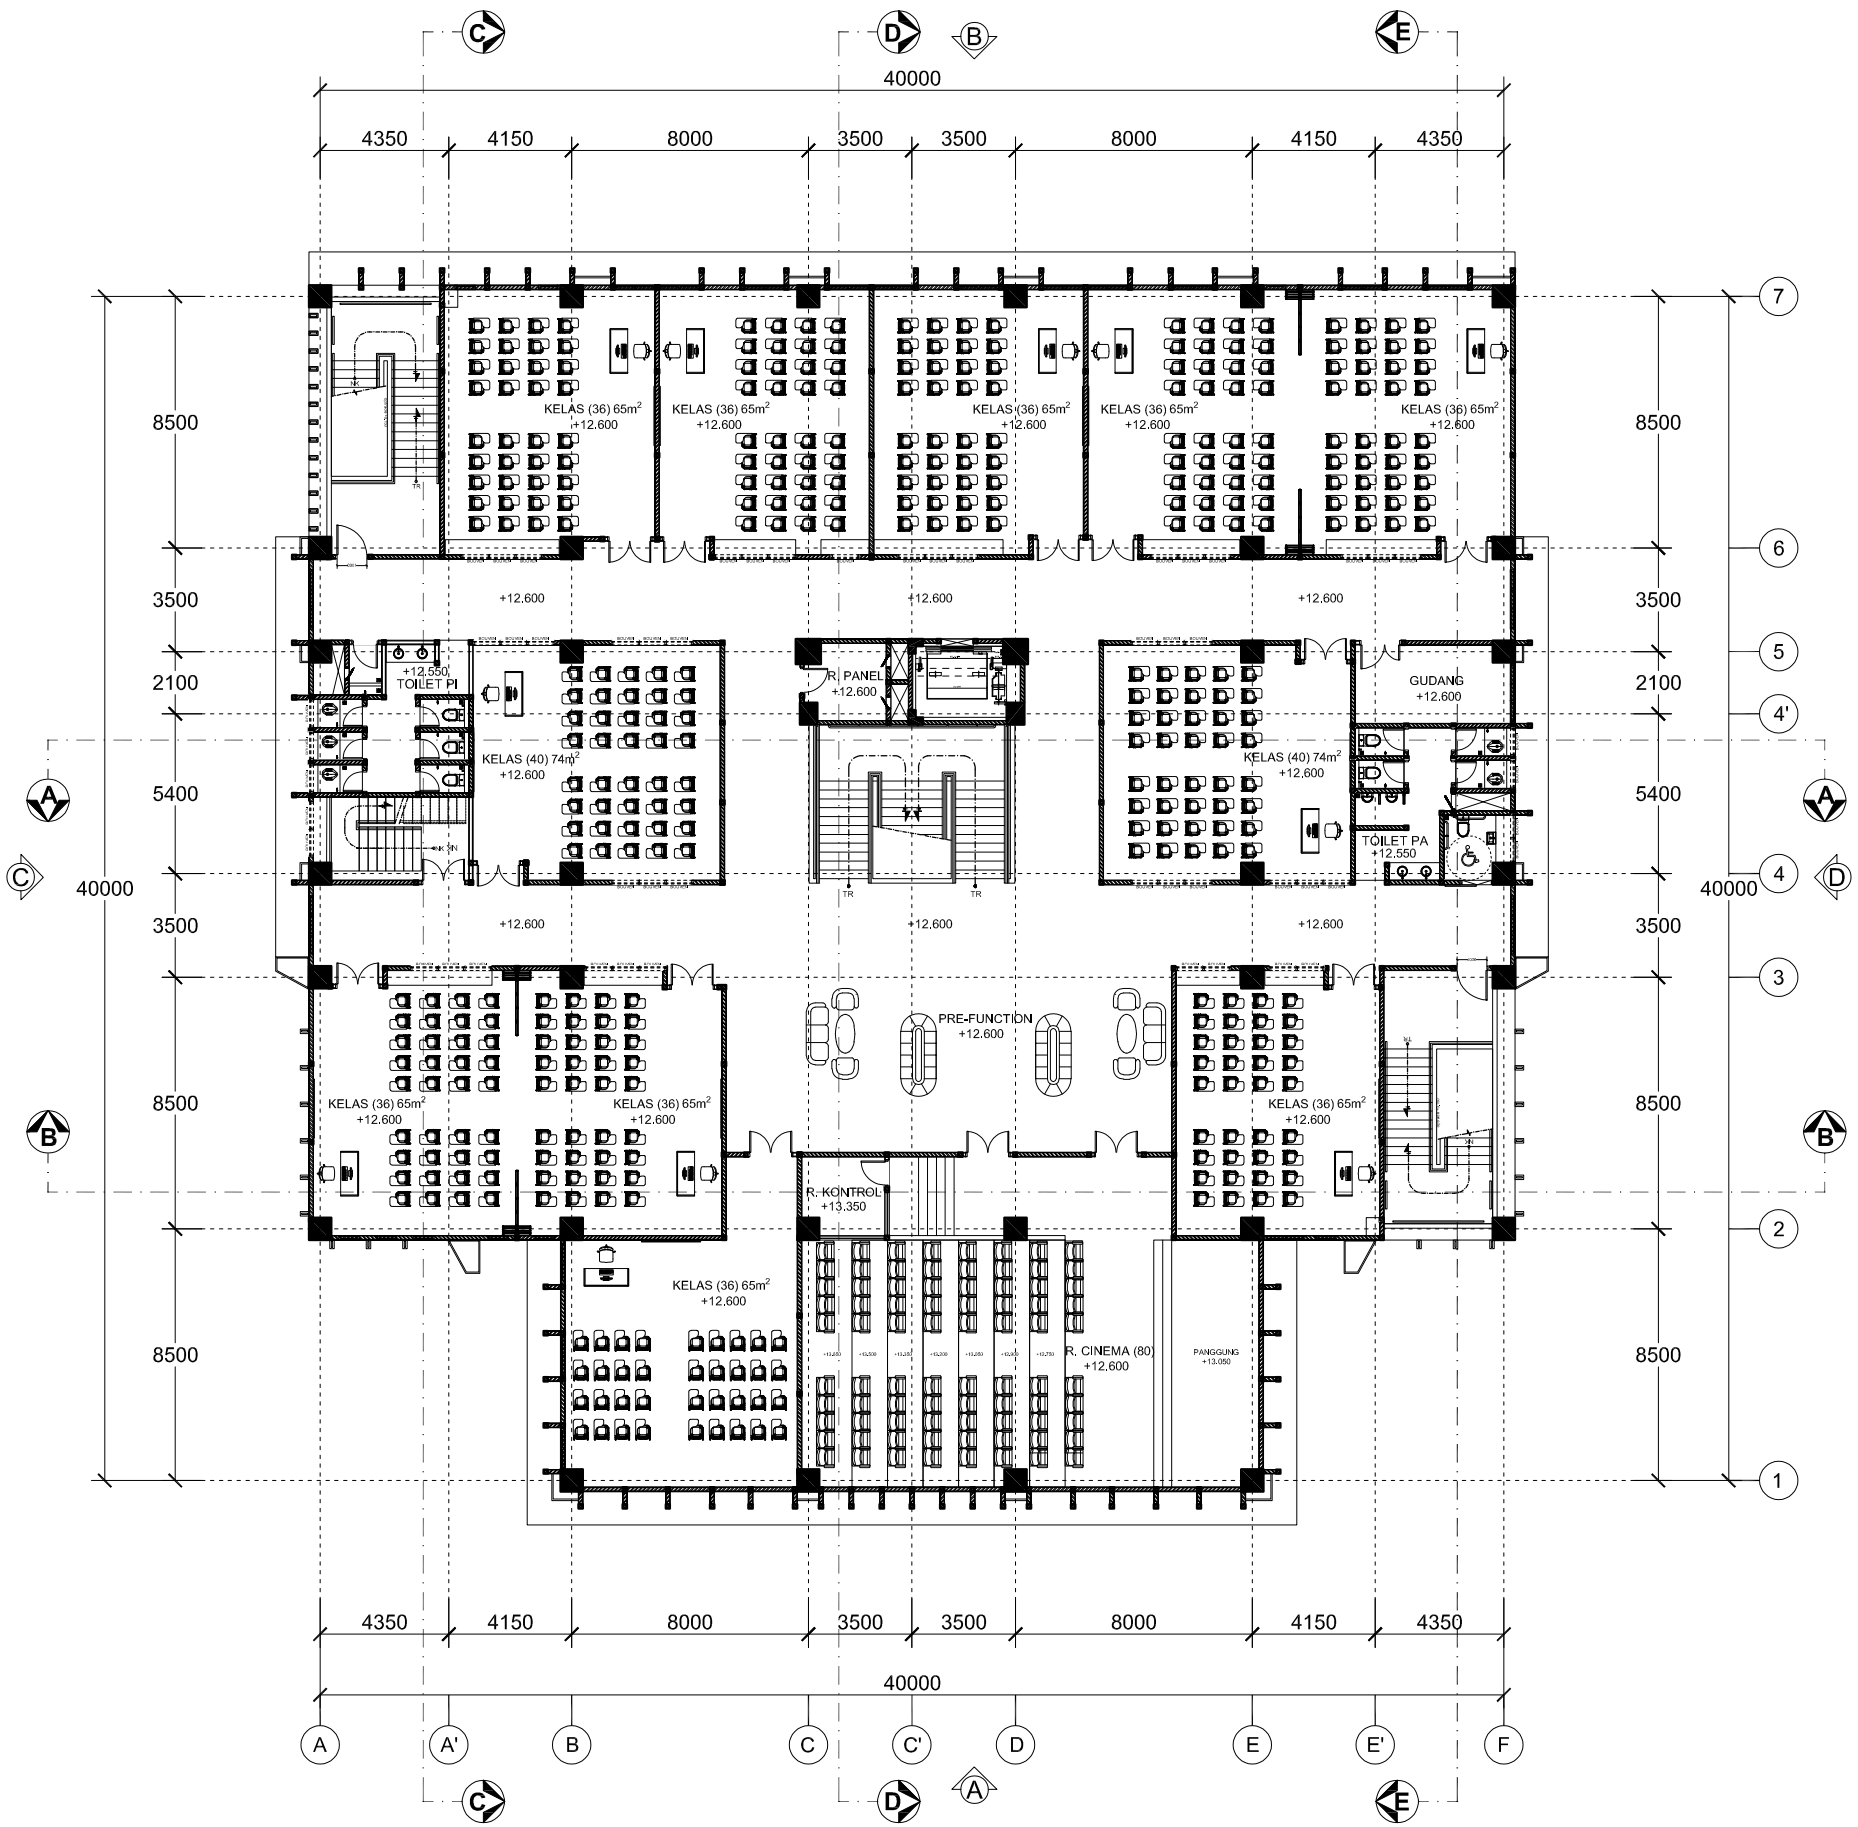


## DENAH LANTAI 04

SKALA 1 : 250

**KEMENTERIAN AGAMA REPUBLIK INDONESIA**
**UNIVERSITAS ISLAM NEGERI**
**SJECH M. DJAMIL DJAMBEK**
JL. GURUN AUR KUBANG PUTIH, KABUPATEN AGAM, SUMATERA BARAT

**PEKERJAAN**

PEMBANGUNAN GEDUNG PENDIDIKAN TERPADU

**LOKASI**


JL. GURUN AUR, KENAGARIAN KUBANG PUTIAH, KECAMATAN BANUHAMPU, KABUPATEN AGAM, SUMATERA BARAT

**TAHUN ANGGARAN**

2026

| JUDUL GAMBAR | SKALA |
|---|---|
| DENAH LANTAI 04 | 1 : 250 |

| KODE | NO. LBR | JML. LBR |
|---|---|---|
| ARS | 7 | 162 |

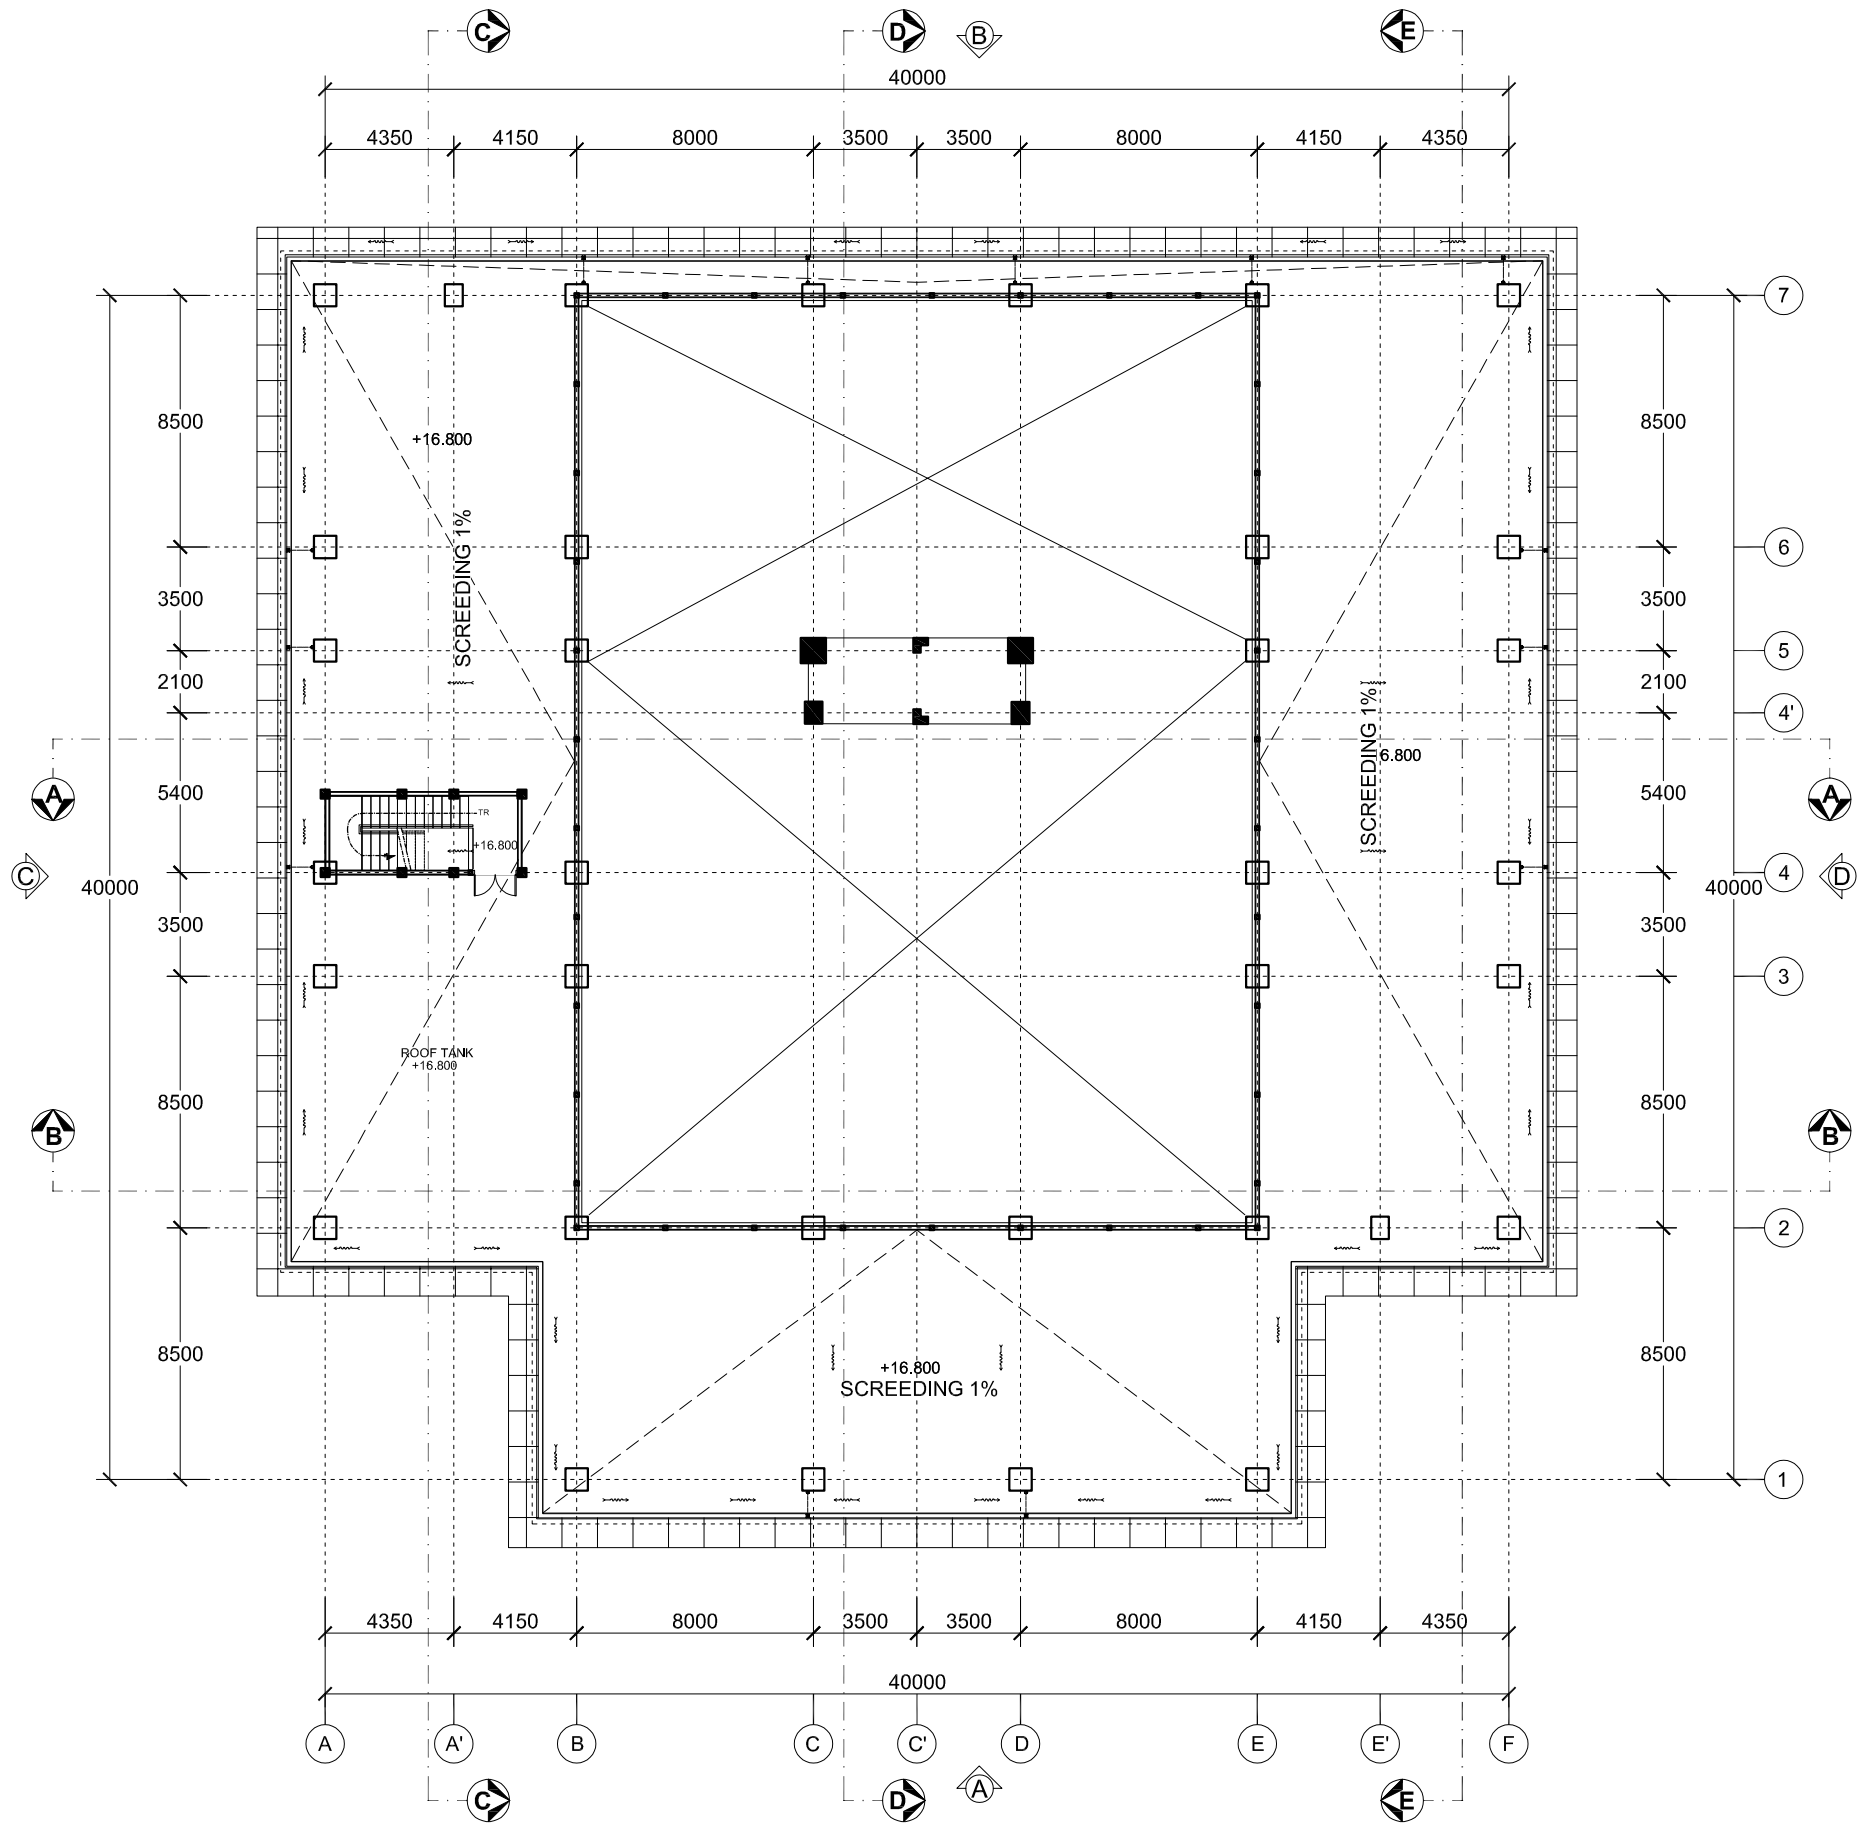


## DENAH LANTAI ATAP

SKALA 1 : 250


UIN
SJECH M. DJAMIL DJAMBEK
BUKITTINGGI

KEMENTERIAN AGAMA REPUBLIK INDONESIA
**UNIVERSITAS ISLAM NEGERI**
**SJECH M. DJAMIL DJAMBEK**
JL. GURUN AUR KUBANG PUTIH, KABUPATEN AGAM, SUMATERA BARAT


**PEKERJAAN**

PEMBANGUNAN GEDUNG PENDIDIKAN TERPADU

**LOKASI**


JL. GURUN AUR, KENAGARIAN KUBANG PUTIAH, KECAMATAN BANUHAMPU, KABUPATEN AGAM, SUMATERA BARAT

**TAHUN ANGGARAN**

2026

| JUDUL GAMBAR | SKALA |
|---|---|
| DENAH LANTAI ATAP | 1 : 250 |

| KODE | NO. LBR | JML. LBR |
|---|---|---|
| ARS | 8 | 162 |

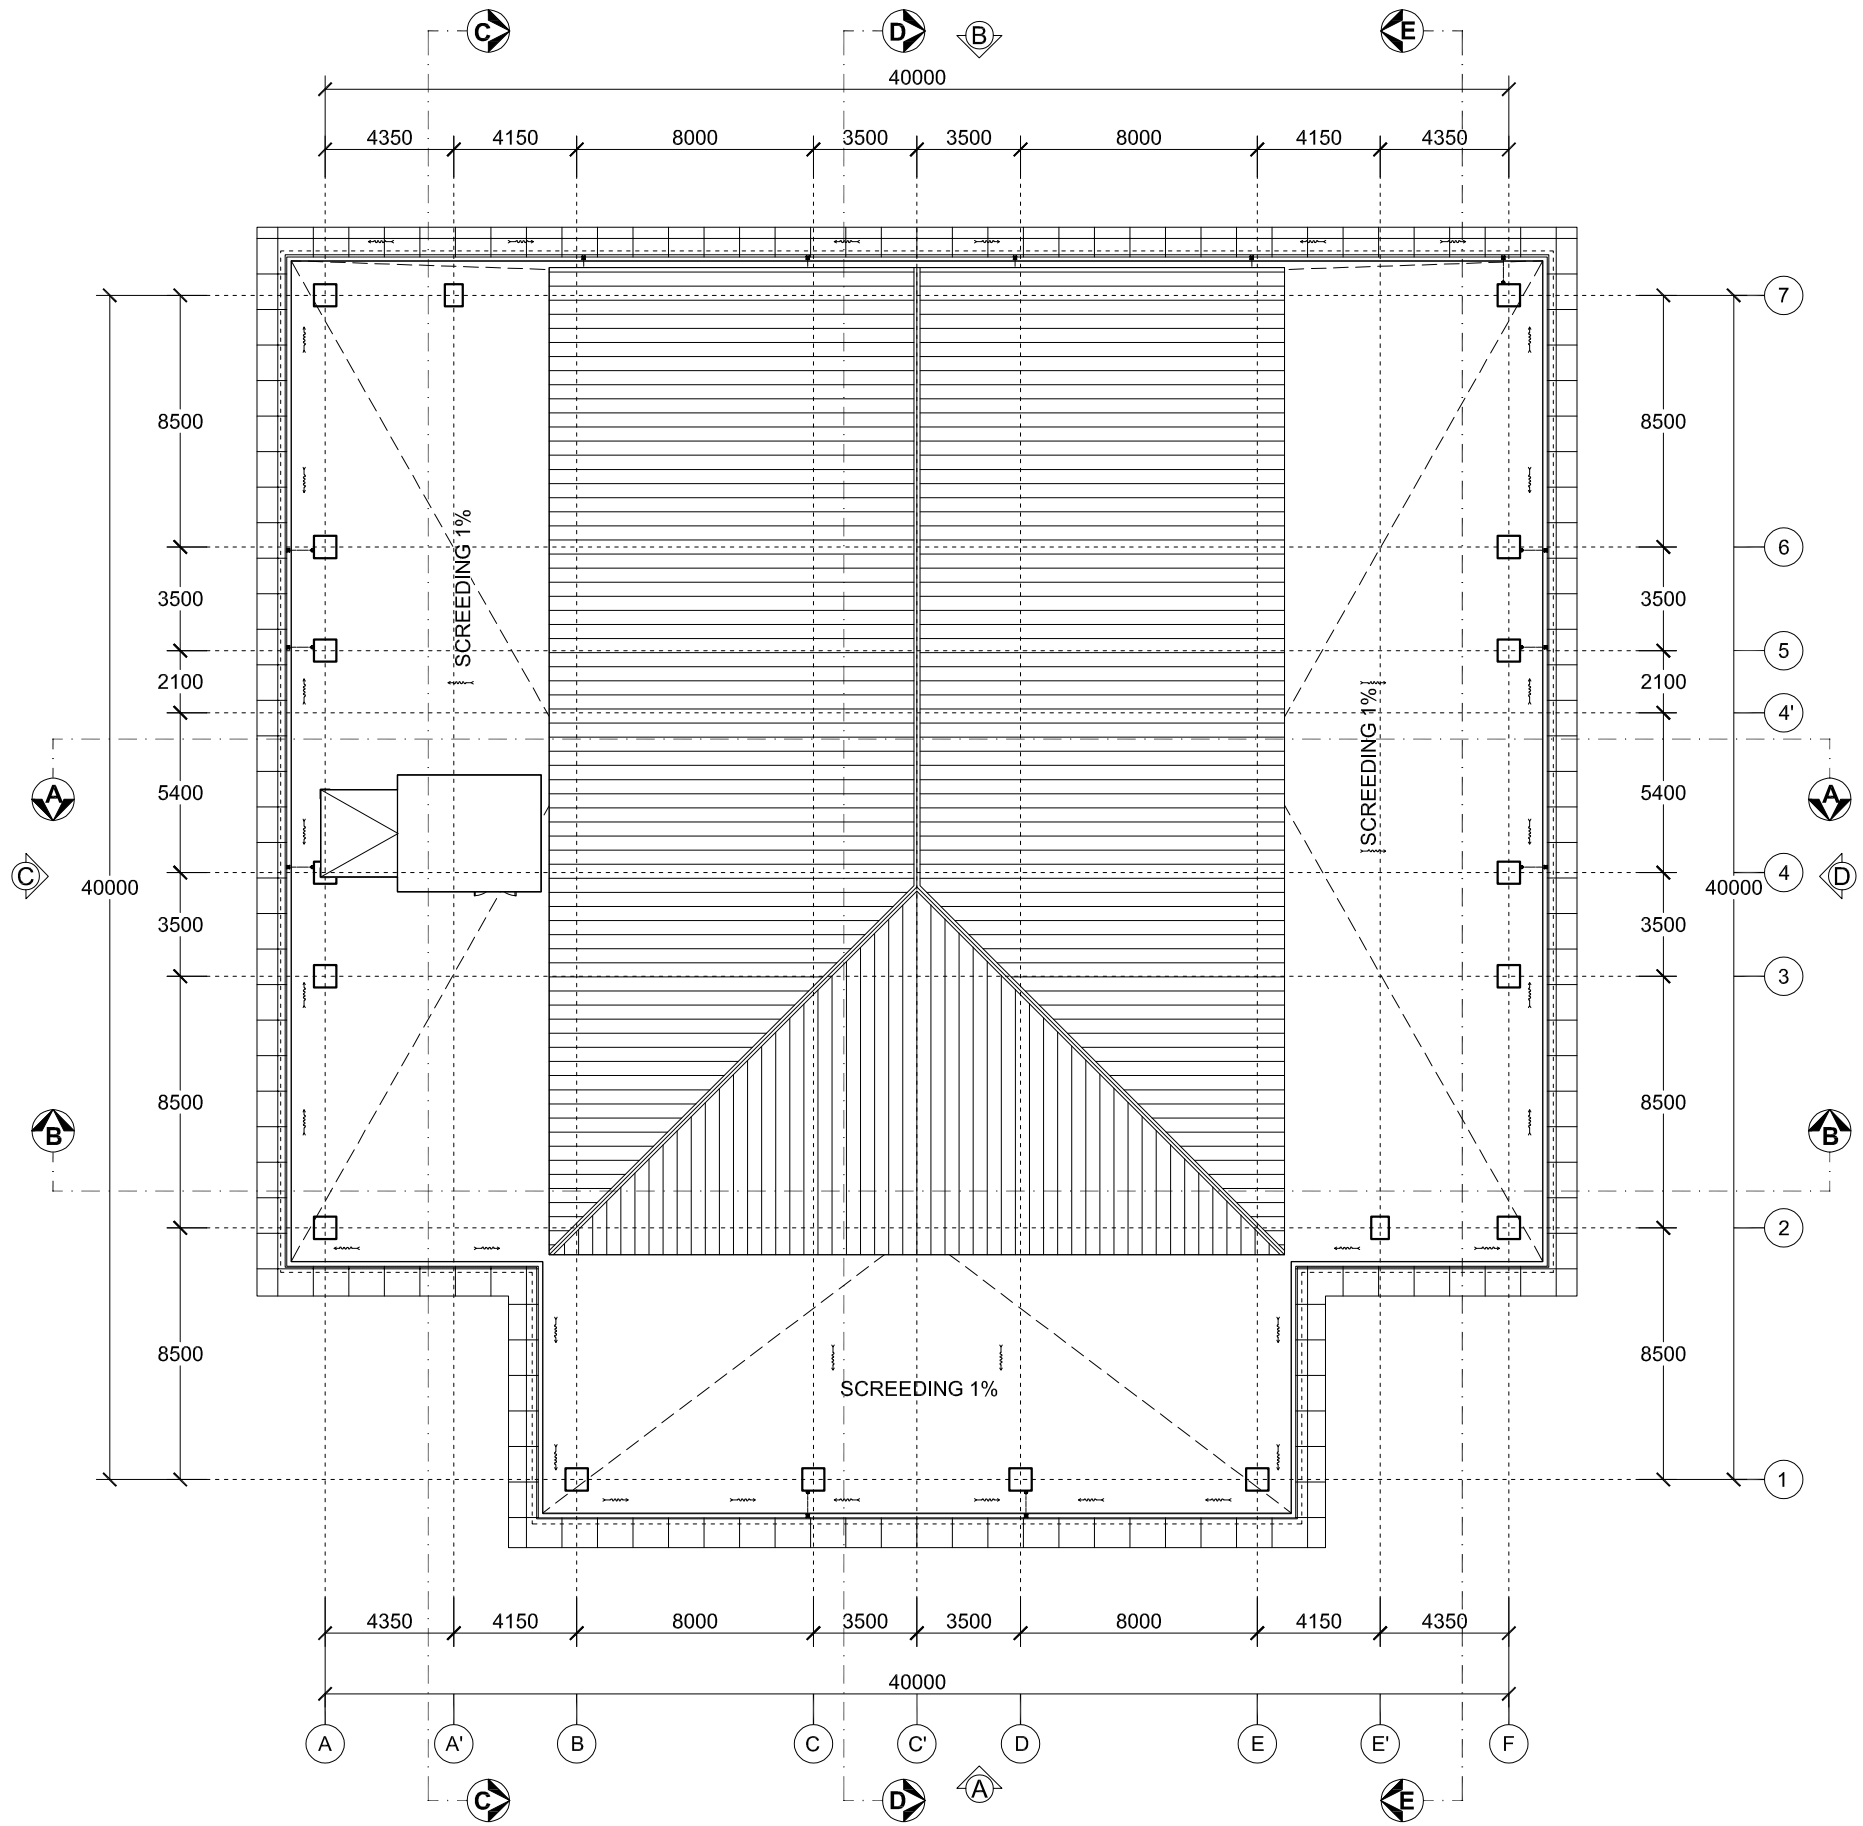


## TAMPAK ATAS

SKALA 1 : 250


UIN
SJECH M. DJAMIL DJAMBEK
BUKITTINGGI

KEMENTERIAN AGAMA REPUBLIK INDONESIA
**UNIVERSITAS ISLAM NEGERI**
**SJECH M. DJAMIL DJAMBEK**
JL. GURUN AUR KUBANG PUTIH, KABUPATEN AGAM, SUMATERA BARAT


**PEKERJAAN**

PEMBANGUNAN GEDUNG PENDIDIKAN TERPADU

**LOKASI**

JL. GURUN AUR, KENAGARIAN KUBANG PUTIAH, KECAMATAN BANUHAMPU, KABUPATEN AGAM, SUMATERA BARAT

**TAHUN ANGGARAN**

2026

| JUDUL GAMBAR | SKALA |
|---|---|
| TAMPAK ATAS | 1 : 250 |

| KODE | NO. LBR | JML. LBR |
|---|---|---|
| ARS | 9 | 162 |




## TAMPAK A

SKALA 1 : 200

UIN
SJECH M. DJAMIL DJAMBEK
BUKITTINGGI

KEMENTERIAN AGAMA REPUBLIK INDONESIA
**UNIVERSITAS ISLAM NEGERI**
**SJECH M. DJAMIL DJAMBEK**
JL. GURUN AUR KUBANG PUTIH, KABUPATEN AGAM, SUMATERA BARAT

**PEKERJAAN**

PEMBANGUNAN GEDUNG PENDIDIKAN TERPADU

**LOKASI**

JL. GURUN AUR, KENAGARIAN KUBANG PUTIAH, KECAMATAN BANUHAMPU, KABUPATEN AGAM, SUMATERA BARAT

**TAHUN ANGGARAN**

2026

| JUDUL GAMBAR | SKALA |
|---|---|
| TAMPAK A | 1 : 200 |

| KODE | NO. LBR | JML. LBR |
|---|---|---|
| ARS | 10 | 162 |




## TAMPAK B

SKALA 1 : 200

UIN
SJECH M. DJAMIL DJAMBEK
BUKITTINGGI

KEMENTERIAN AGAMA REPUBLIK INDONESIA
**UNIVERSITAS ISLAM NEGERI**
**SJECH M. DJAMIL DJAMBEK**
JL. GURUN AUR KUBANG PUTIH, KABUPATEN AGAM, SUMATERA BARAT

**PEKERJAAN**

PEMBANGUNAN GEDUNG PENDIDIKAN TERPADU

**LOKASI**


JL. GURUN AUR, KENAGARIAN KUBANG PUTIAH, KECAMATAN BANUHAMPU, KABUPATEN AGAM, SUMATERA BARAT

**TAHUN ANGGARAN**

2026

| JUDUL GAMBAR | SKALA |
|---|---|
| TAMPAK B | 1 : 200 |

| KODE | NO. LBR | JML. LBR |
|---|---|---|
| ARS | 11 | 162 |

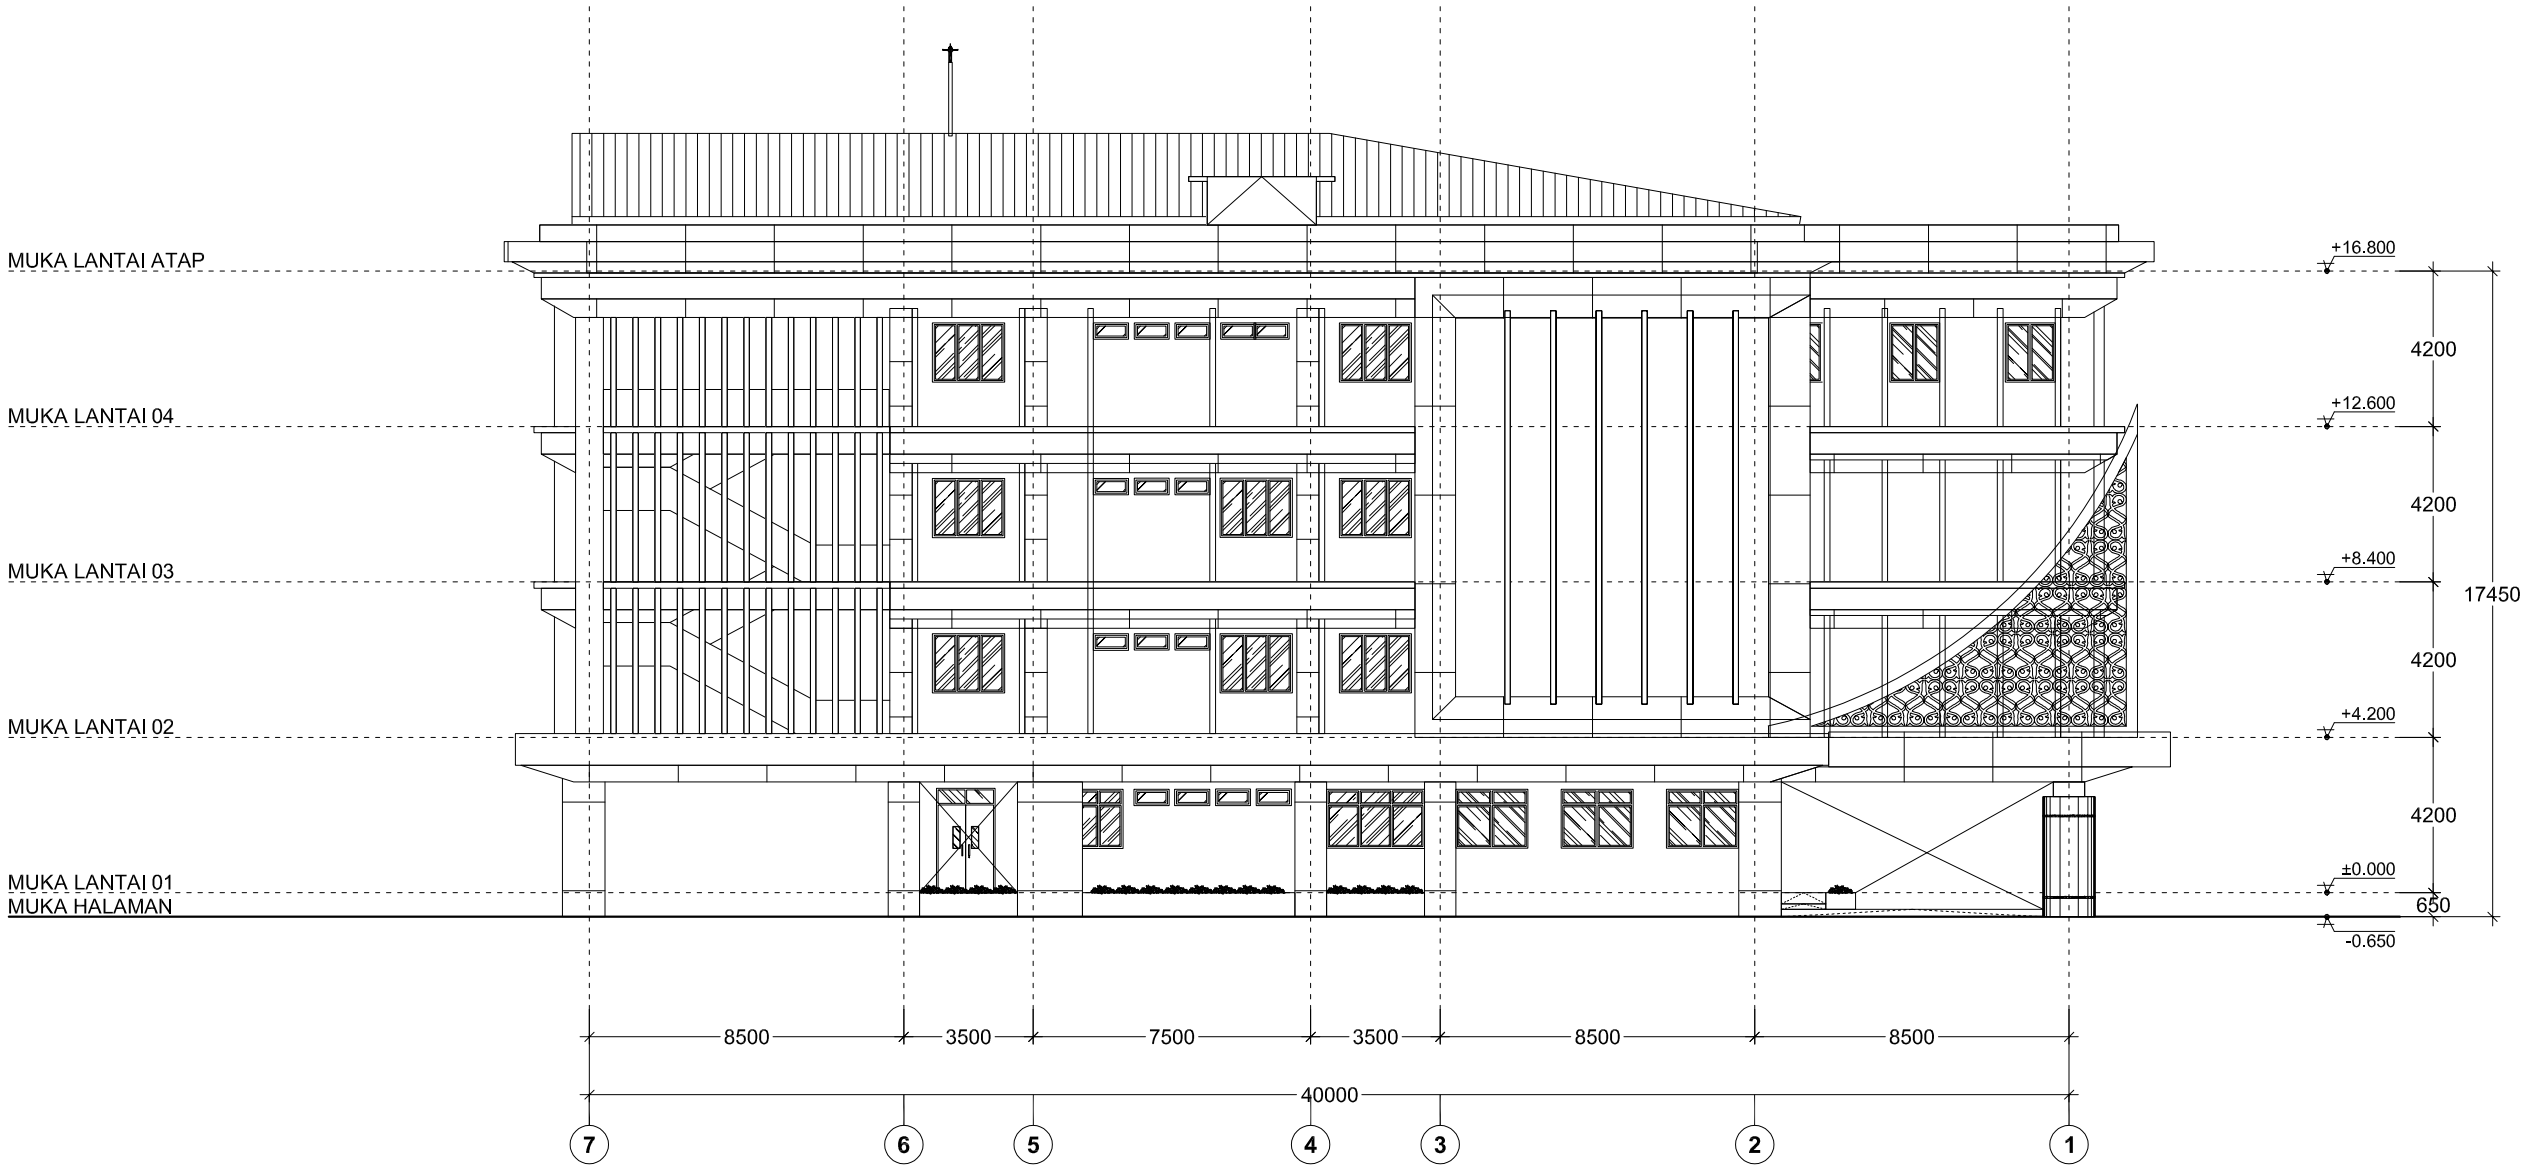


## TAMPAK C

SKALA 1 : 200

KEMENTERIAN AGAMA REPUBLIK INDONESIA
UNIVERSITAS ISLAM NEGERI
SJECH M. DJAMIL DJAMBEK
JL. GURUN AUR KUBANG PUTIH, KABUPATEN AGAM, SUMATERA BARAT

**PEKERJAAN**

PEMBANGUNAN GEDUNG PENDIDIKAN TERPADU

**LOKASI**


JL. GURUN AUR, KENAGARIAN KUBANG PUTIAH, KECAMATAN BANUHAMPU, KABUPATEN AGAM, SUMATERA BARAT

**TAHUN ANGGARAN**

2026

| JUDUL GAMBAR | SKALA |
|---|---|
| TAMPAK C | 1 : 200 |

| KODE | NO. LBR | JML. LBR |
|---|---|---|
| ARS | 12 | 162 |

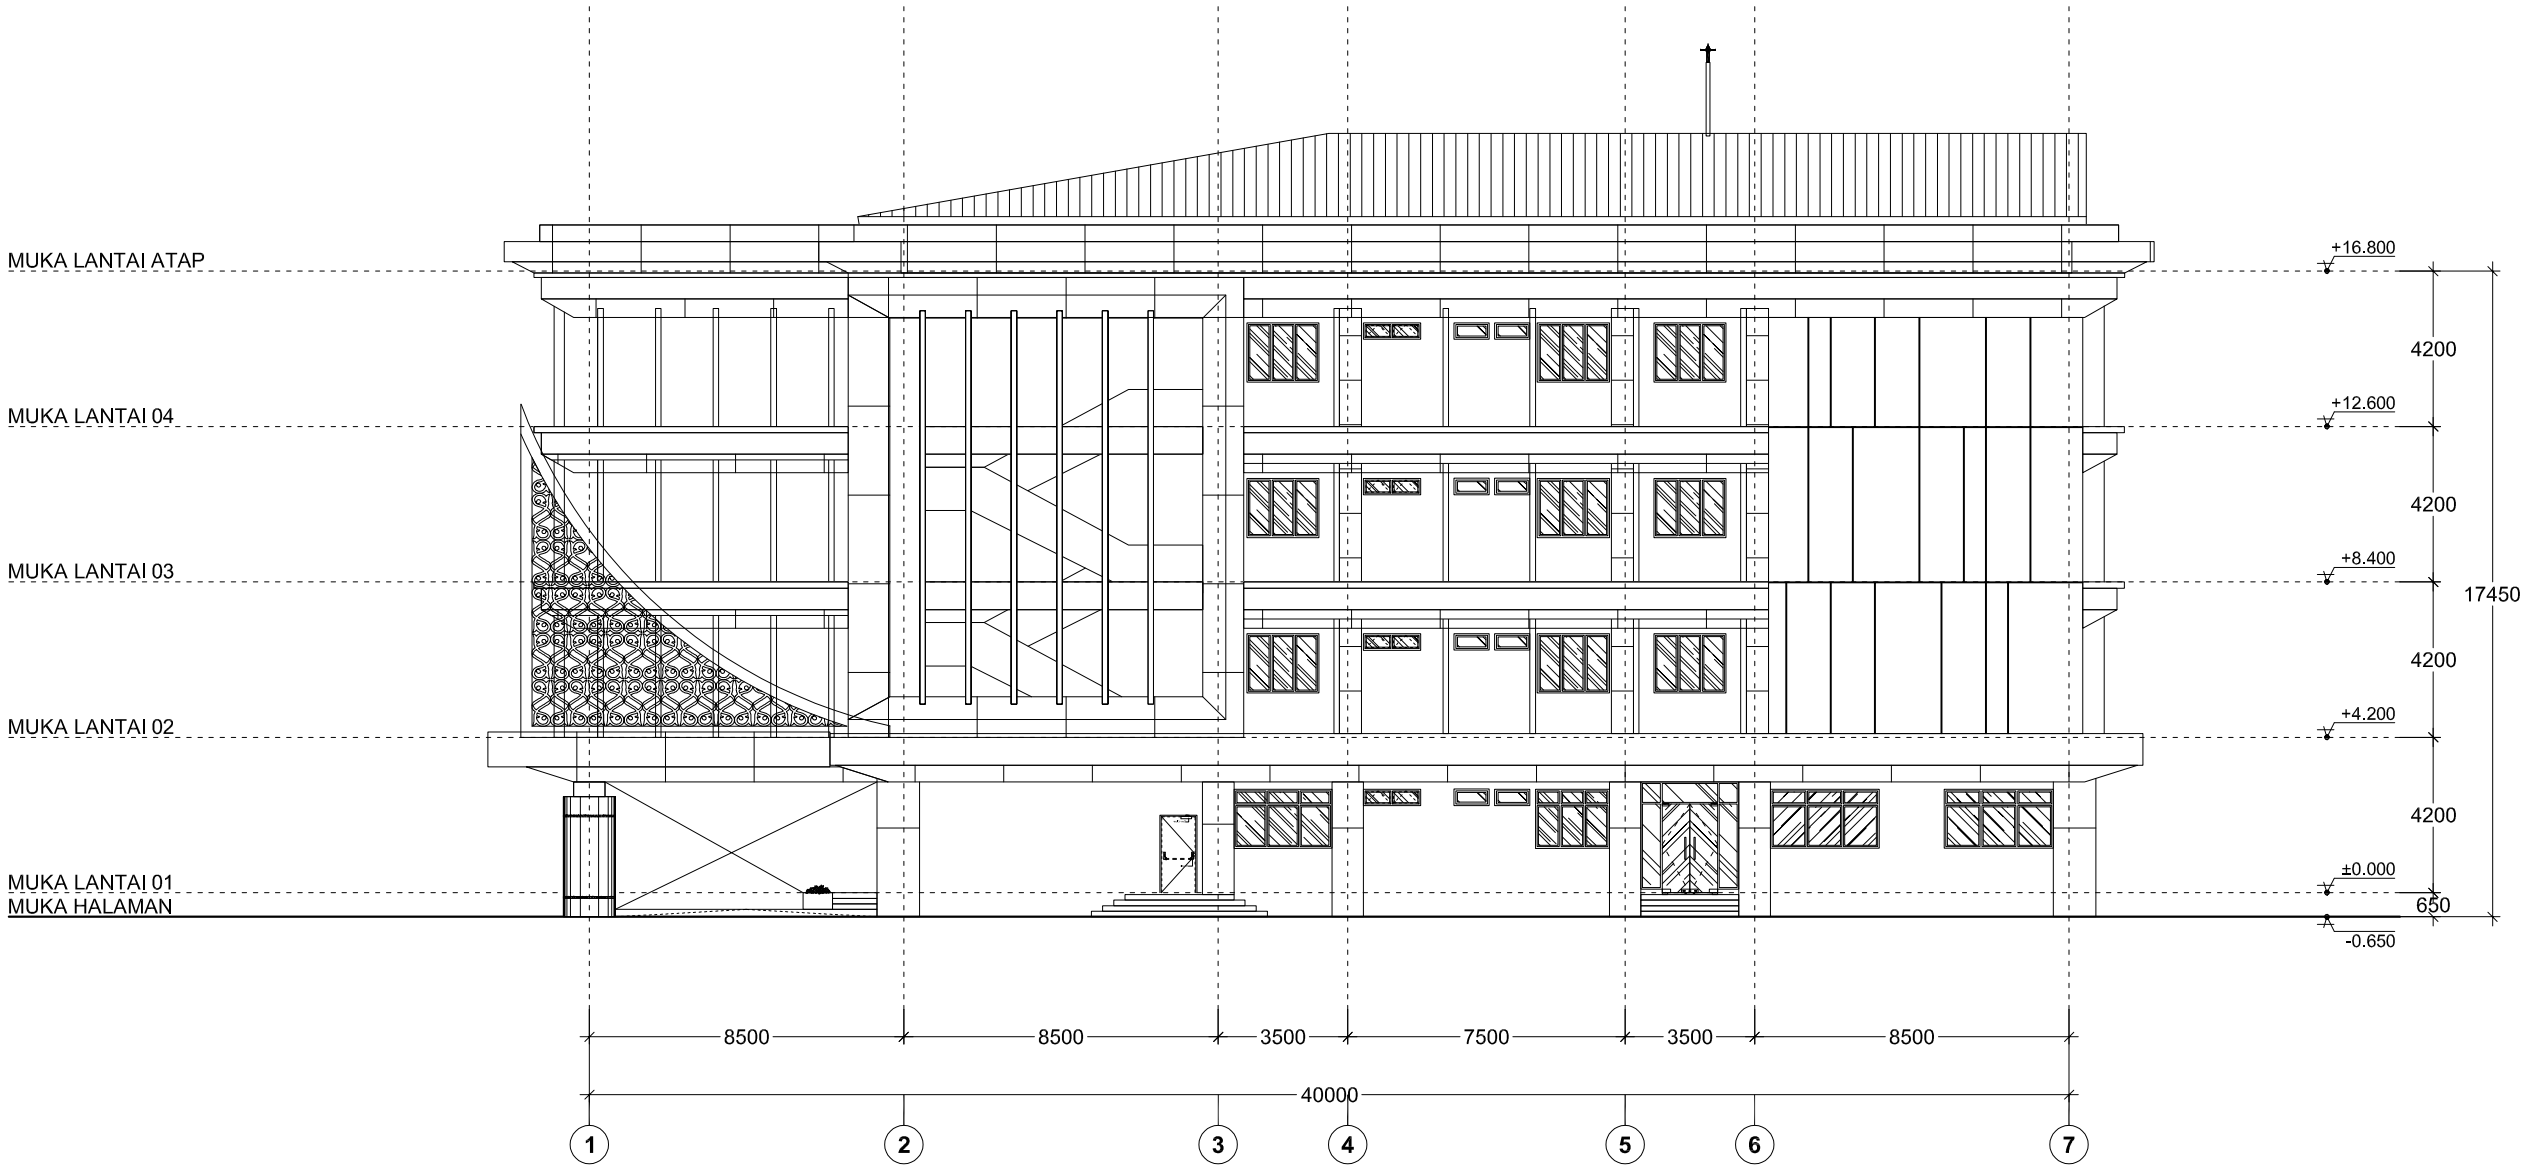


## TAMPAK D

SKALA 1 : 200


UIN
SJECH M. DJAMIL DJAMBEK
BUKITTINGGI

KEMENTERIAN AGAMA REPUBLIK INDONESIA
UNIVERSITAS ISLAM NEGERI
SJECH M. DJAMIL DJAMBEK
JL. GURUN AUR KUBANG PUTIH, KABUPATEN AGAM, SUMATERA BARAT


**PEKERJAAN**

PEMBANGUNAN GEDUNG PENDIDIKAN TERPADU

**LOKASI**

JL. GURUN AUR, KENAGARIAN KUBANG PUTIAH, KECAMATAN BANUHAMPU, KABUPATEN AGAM, SUMATERA BARAT

**TAHUN ANGGARAN**

2026

| JUDUL GAMBAR | SKALA |
|---|---|
| TAMPAK D | 1 : 200 |

| KODE | NO. LBR | JML. LBR |
|---|---|---|
| ARS | 13 | 162 |